



户用离网光伏发电系统——系统电气主接线图

拉萨/兰州/哈尔滨差异化设计（兰州） · A3

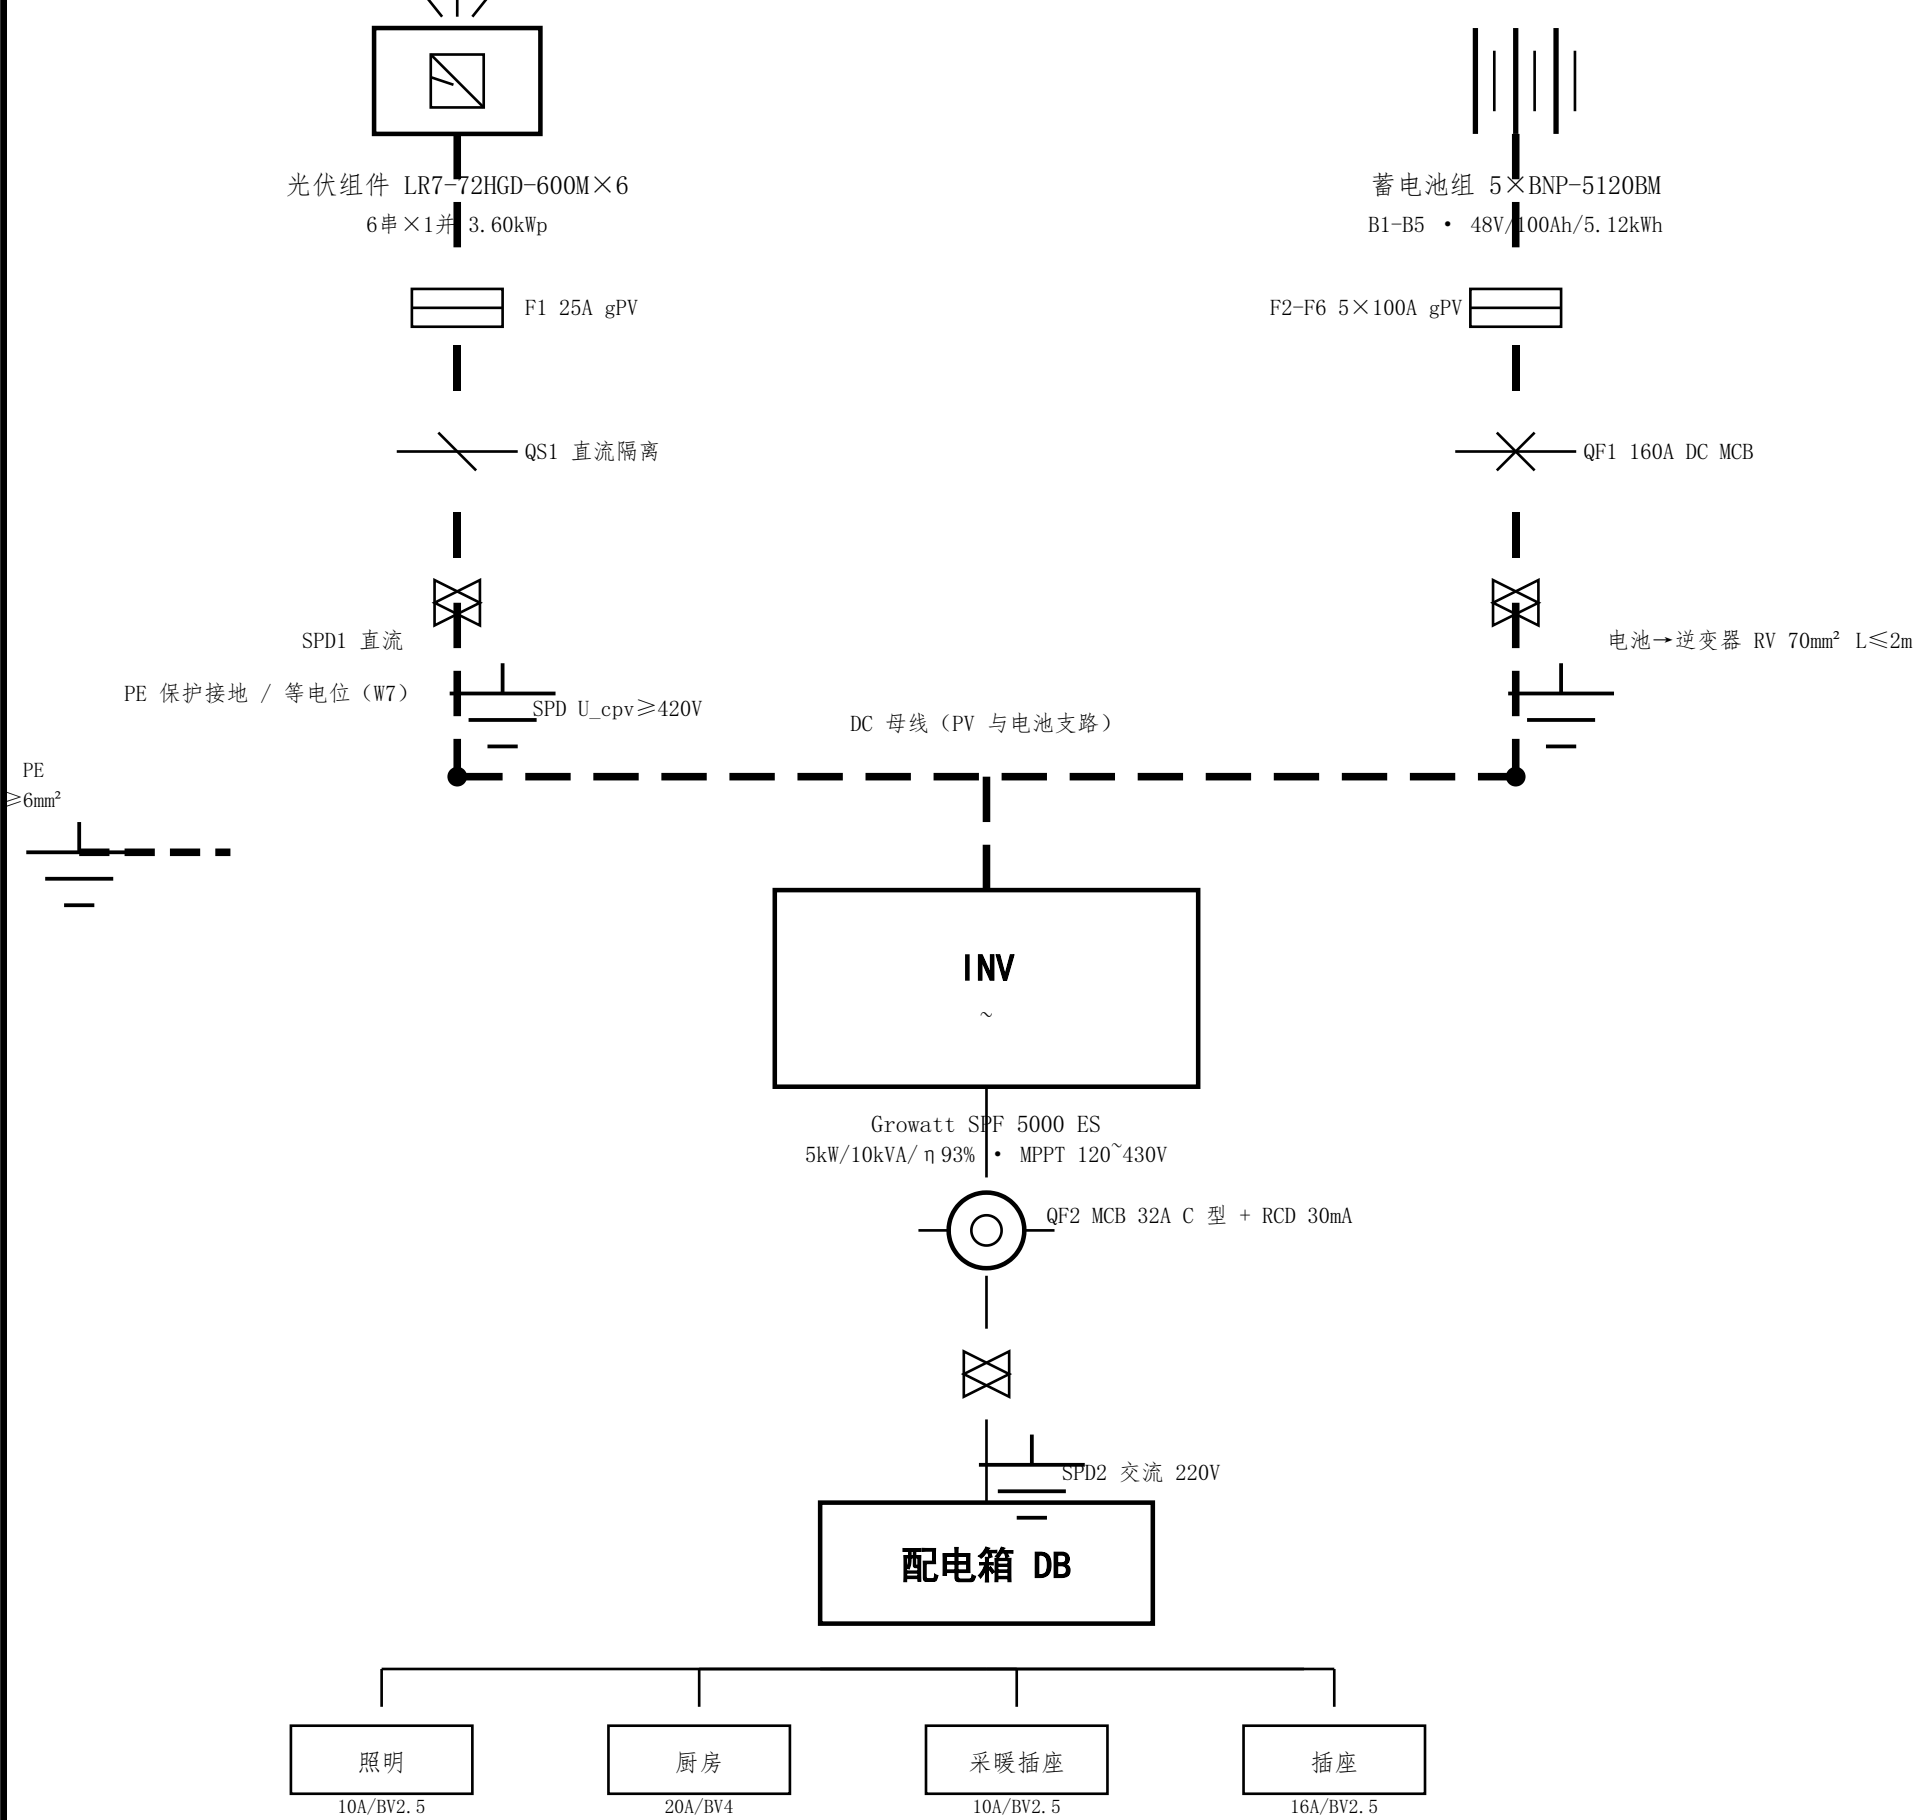


图例 /

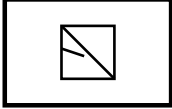


光伏组件




蓄电池

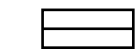

熔断器 FU

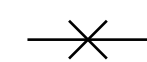


断路器 QF

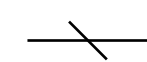

隔离开关 QS



SPD 防雷器

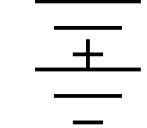

接地



直流（虚线）



交流（实线）



PE（短划线）

说明：

1. 单线图，保护配置见 W7；
2. 蓄电池→逆变器按 45V 校核压降（红线）；
3. 光伏支路 PV1-F 4mm²；交流 RVV 3×6mm²；
4. 采暖插座为新增回路（10A/2.5mm²）；
5. 接地电阻≤4Ω，等电位联结。

哈尔滨工业大学	系统电气主接线图	图号	T1-01
设计：____	制图：____	审核：____	日期 2026-09-03
学号：____	班级：____	版本 A	页次 1/1
比例	无比例	单位：mm	