



户用离网光伏发电系统——系统电气主接线图

拉萨/兰州/哈尔滨差异化设计（拉萨） · A3

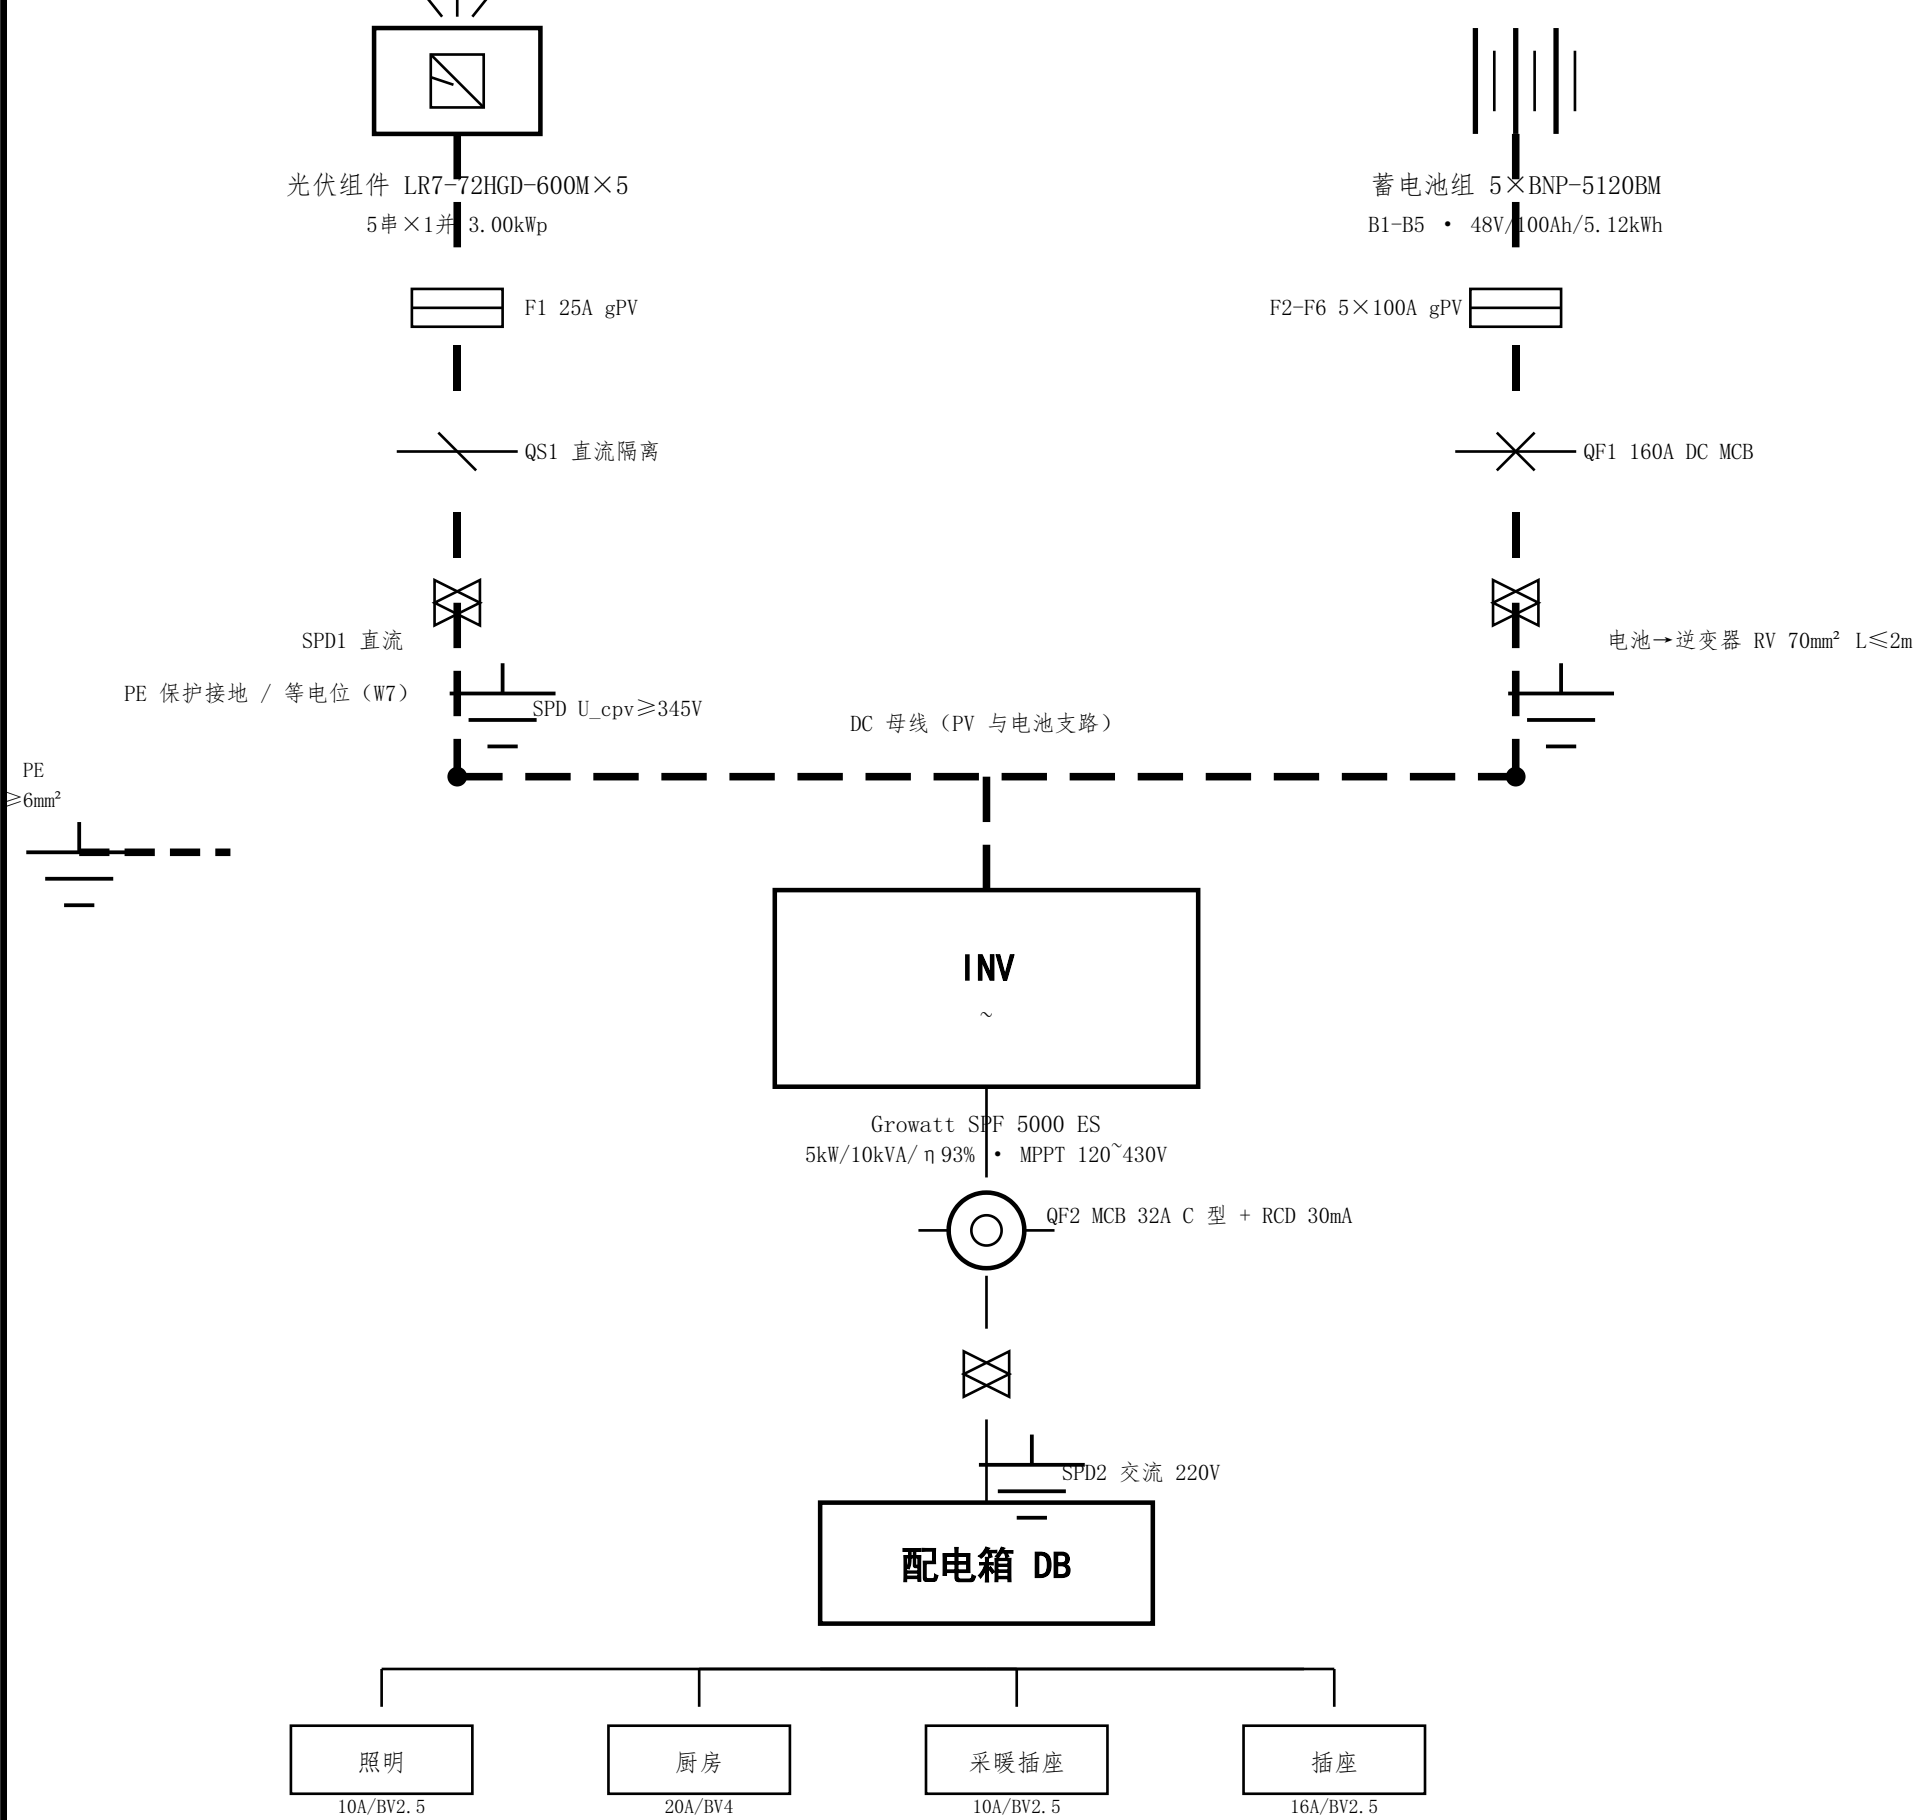


图例 /

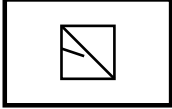


光伏组件




蓄电池

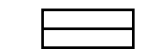

熔断器 FU

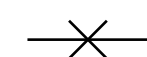

断路器 QF

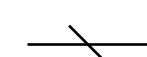


隔离开关 QS




SPD 防雷器



接地

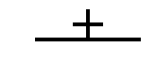

直流 (虚线)

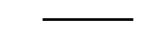

交流 (实线)



PE (短划线)

说明:

- 单线图, 保护配置见 W7;
- 蓄电池→逆变器按 45V 校核压降 (红线);
- 光伏支路 PV1-F 4mm²; 交流 RVV 3×6mm²;
- 采暖插座为新增回路 (10A/2.5mm²);
- 接地电阻≤4Ω, 等电位联结。

哈尔滨工业大学	系统电气主接线图	图号	T1-01
设计: ____	制图: ____	审核: ____	日期 2026-09-03
学号: ____	班级: ____	版本 A	页次 1/1
比例	无比例	单位: mm	