


户用离网光伏发电系统——光伏阵列及支架布置图

拉萨/兰州/哈尔滨差异化设计（哈尔滨） · A3

屋面平面（可用安装区 12m×6m，南向）

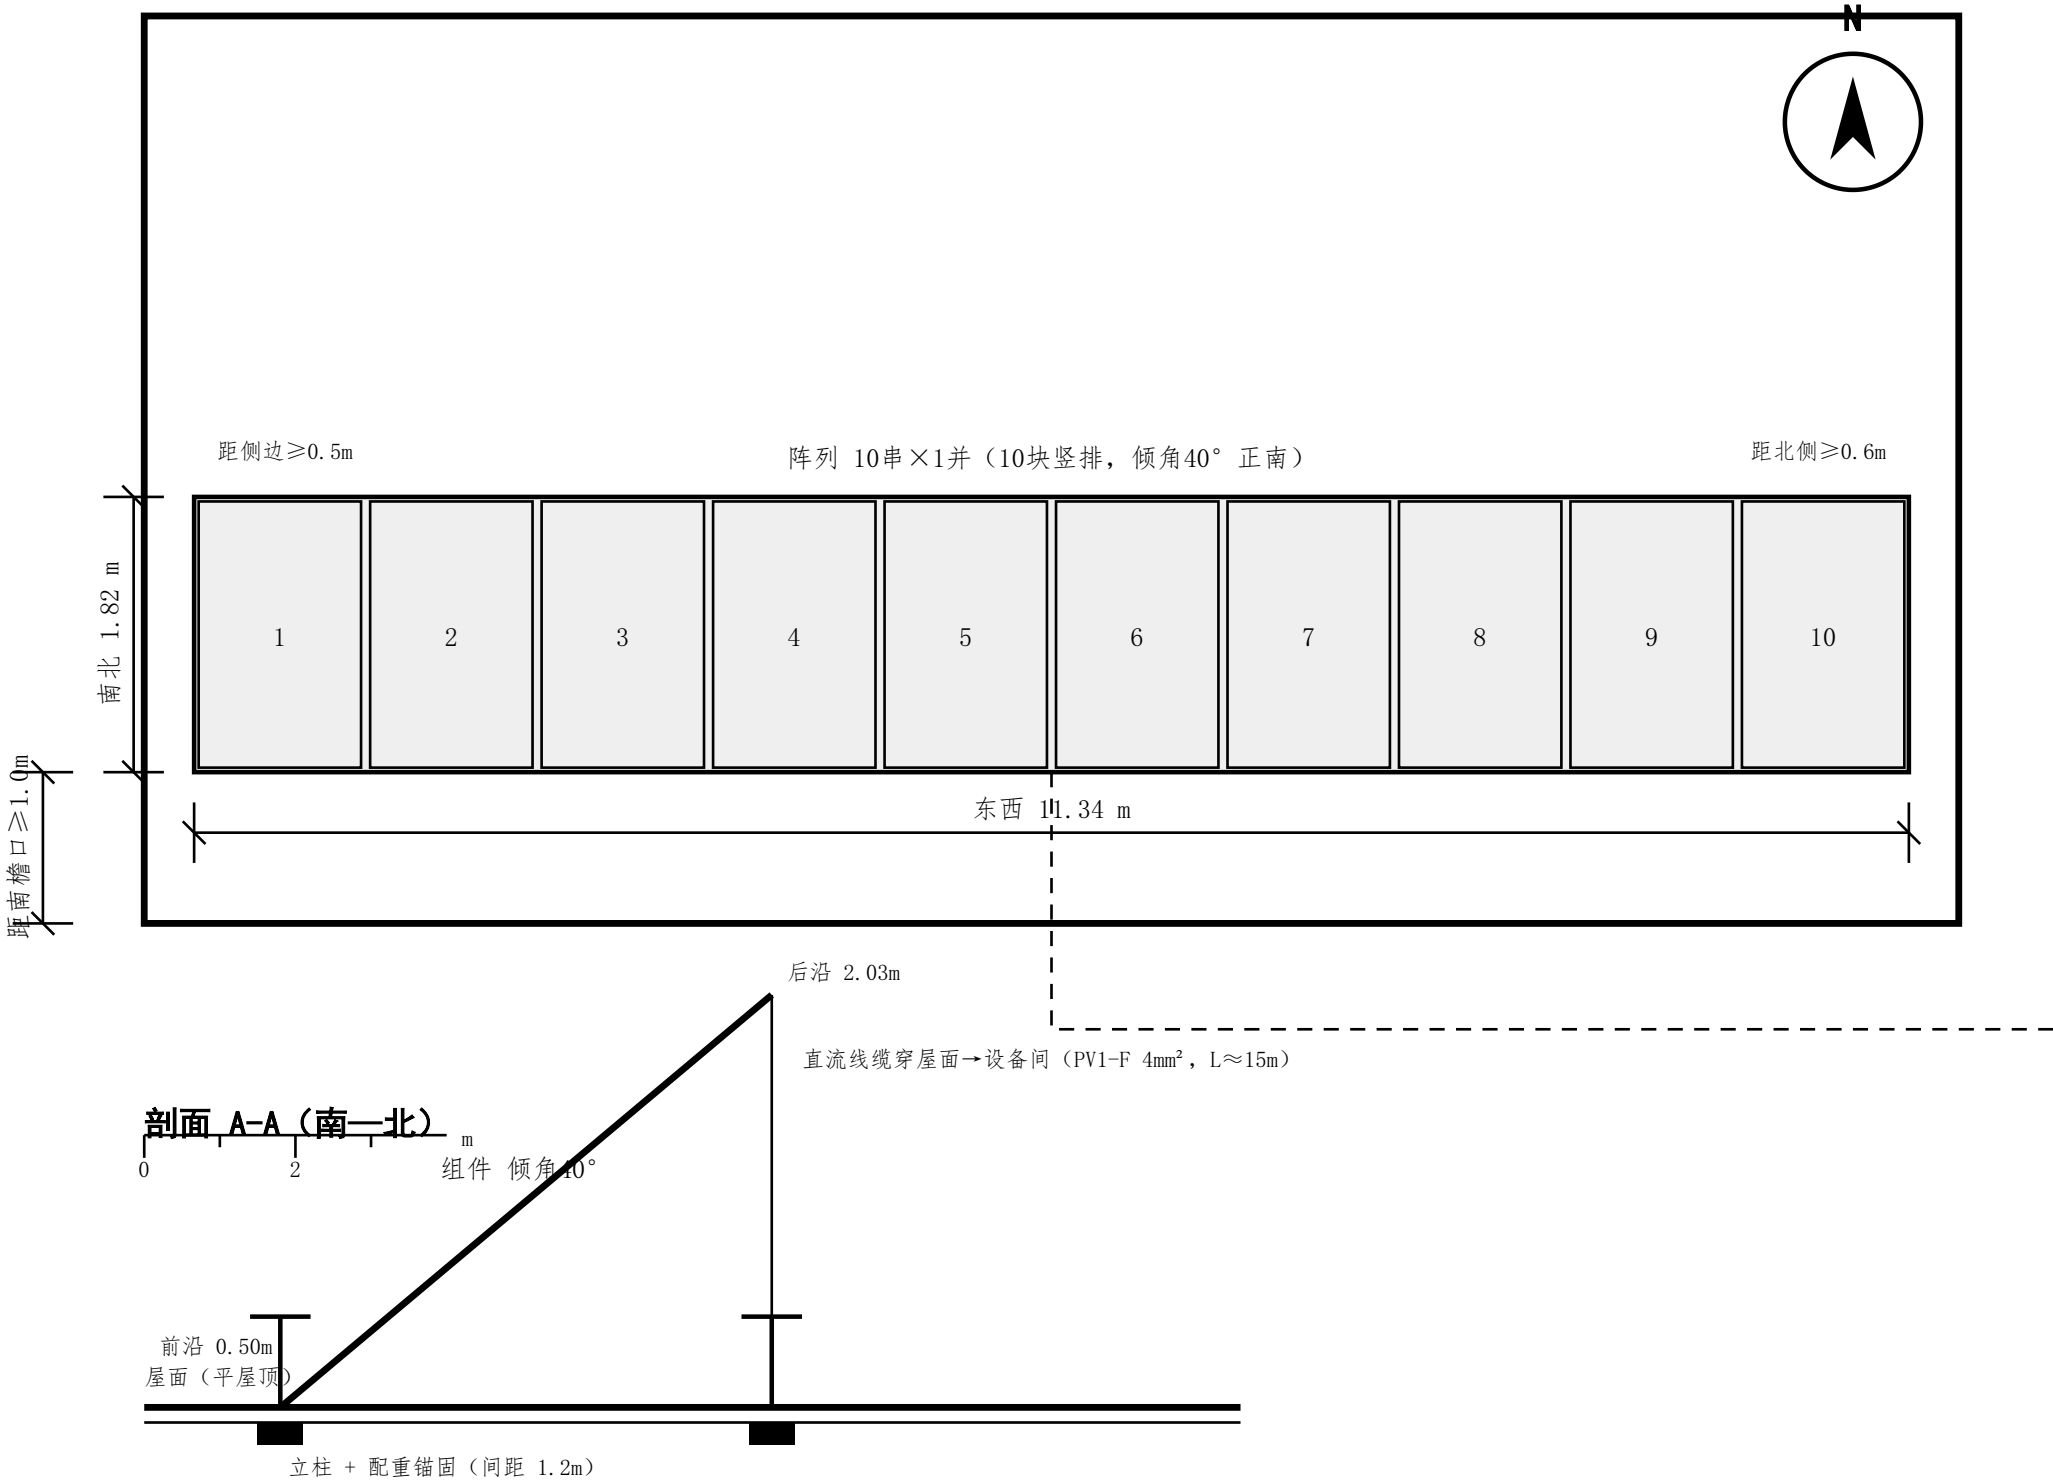

排间间距（扩排）： $D = L \cdot \cos 40^\circ + L \cdot \sin 40^\circ / \tan \alpha_s = 10.88 \text{ m}$ （ $\approx 4.57 \times L$ ）

支架与基础说明：

支架校核（GB 50009，导轨铝 6063-T5， $L_b=1.2\text{m}$ ）： $\sigma=19.2 \text{ MPa} \leq 85 \text{ MPa}$ ， $f=0.61 \text{ mm} \leq L/200$
组件隆基 LR7-72HGD-600M（1134×2382mm，600W）； $w_0=0.55$ ；组合雪载 $s_0=0.45$ 、 $\mu_r=0.5$ （40° 斜面）
基础：屋面配重式（抗倾覆）；阵列下方留 30mm 通风间隙，组件边框与支架可靠接地

哈尔滨工业大学	光伏阵列及支架布置图	图号	T1-02
设计：____	制图：____	审核：____	日期 2026-09-03
学号：____	班级：____	版本 A	页次 1/1
比例	1:100	单位：mm	