
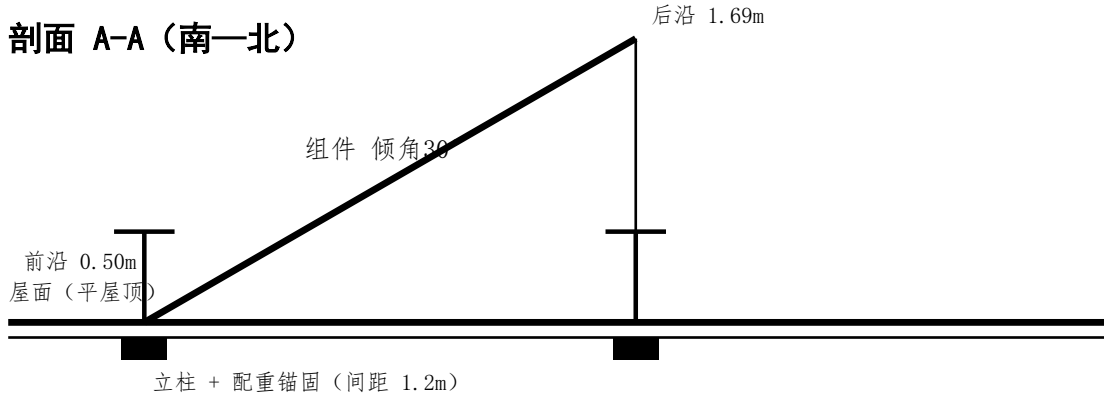
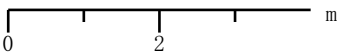


户用离网光伏发电系统——光伏阵列及支架布置图

拉萨/兰州/哈尔滨差异化设计（拉萨） · A3
屋面平面（可用安装区 6m×5m，南向）

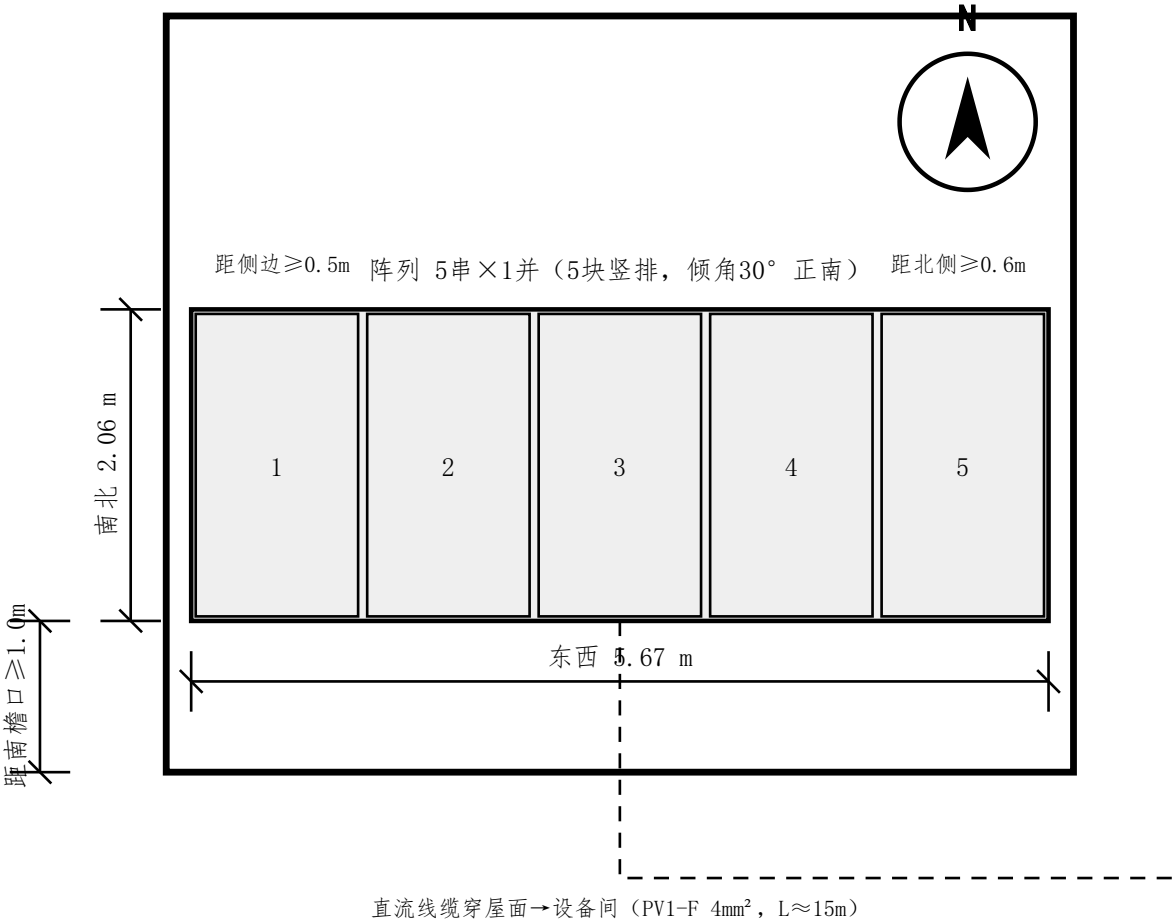

排间间距（扩排）： $D = L \cdot \cos 30^\circ + L \cdot \sin 30^\circ / \tan \alpha_s = 5.09 \text{ m}$ （ $\approx 2.13 \times L$ ）

支架与基础说明：

支架校核（GB 50009，导轨铝 6063-T5， $L_b=1.2\text{m}$ ）： $\sigma=5.6 \text{ MPa} \leq 85\text{MPa}$ ， $f=0.21 \text{ mm} \leq L/200$
组件隆基 LR7-72HGD-600M（1134×2382mm，600W）； $w_0=0.15$ ；高原日照强/少雷区，支架耐候涂装
基础：屋面配重式（抗倾覆）；阵列下方留 30mm 通风间隙，组件边框与支架可靠接地

哈尔滨工业大学	光伏阵列及支架布置图	图号	T1-02
设计：____	制图：____	审核：____	日期 2026-09-03
学号：____	班级：____	版本 A	页次 1/1
比例	1:100	单位：mm	