


# 户用离网光伏发电系统——设备间平面及安装接线图

拉萨/兰州/哈尔滨差异化设计（兰州） · A3

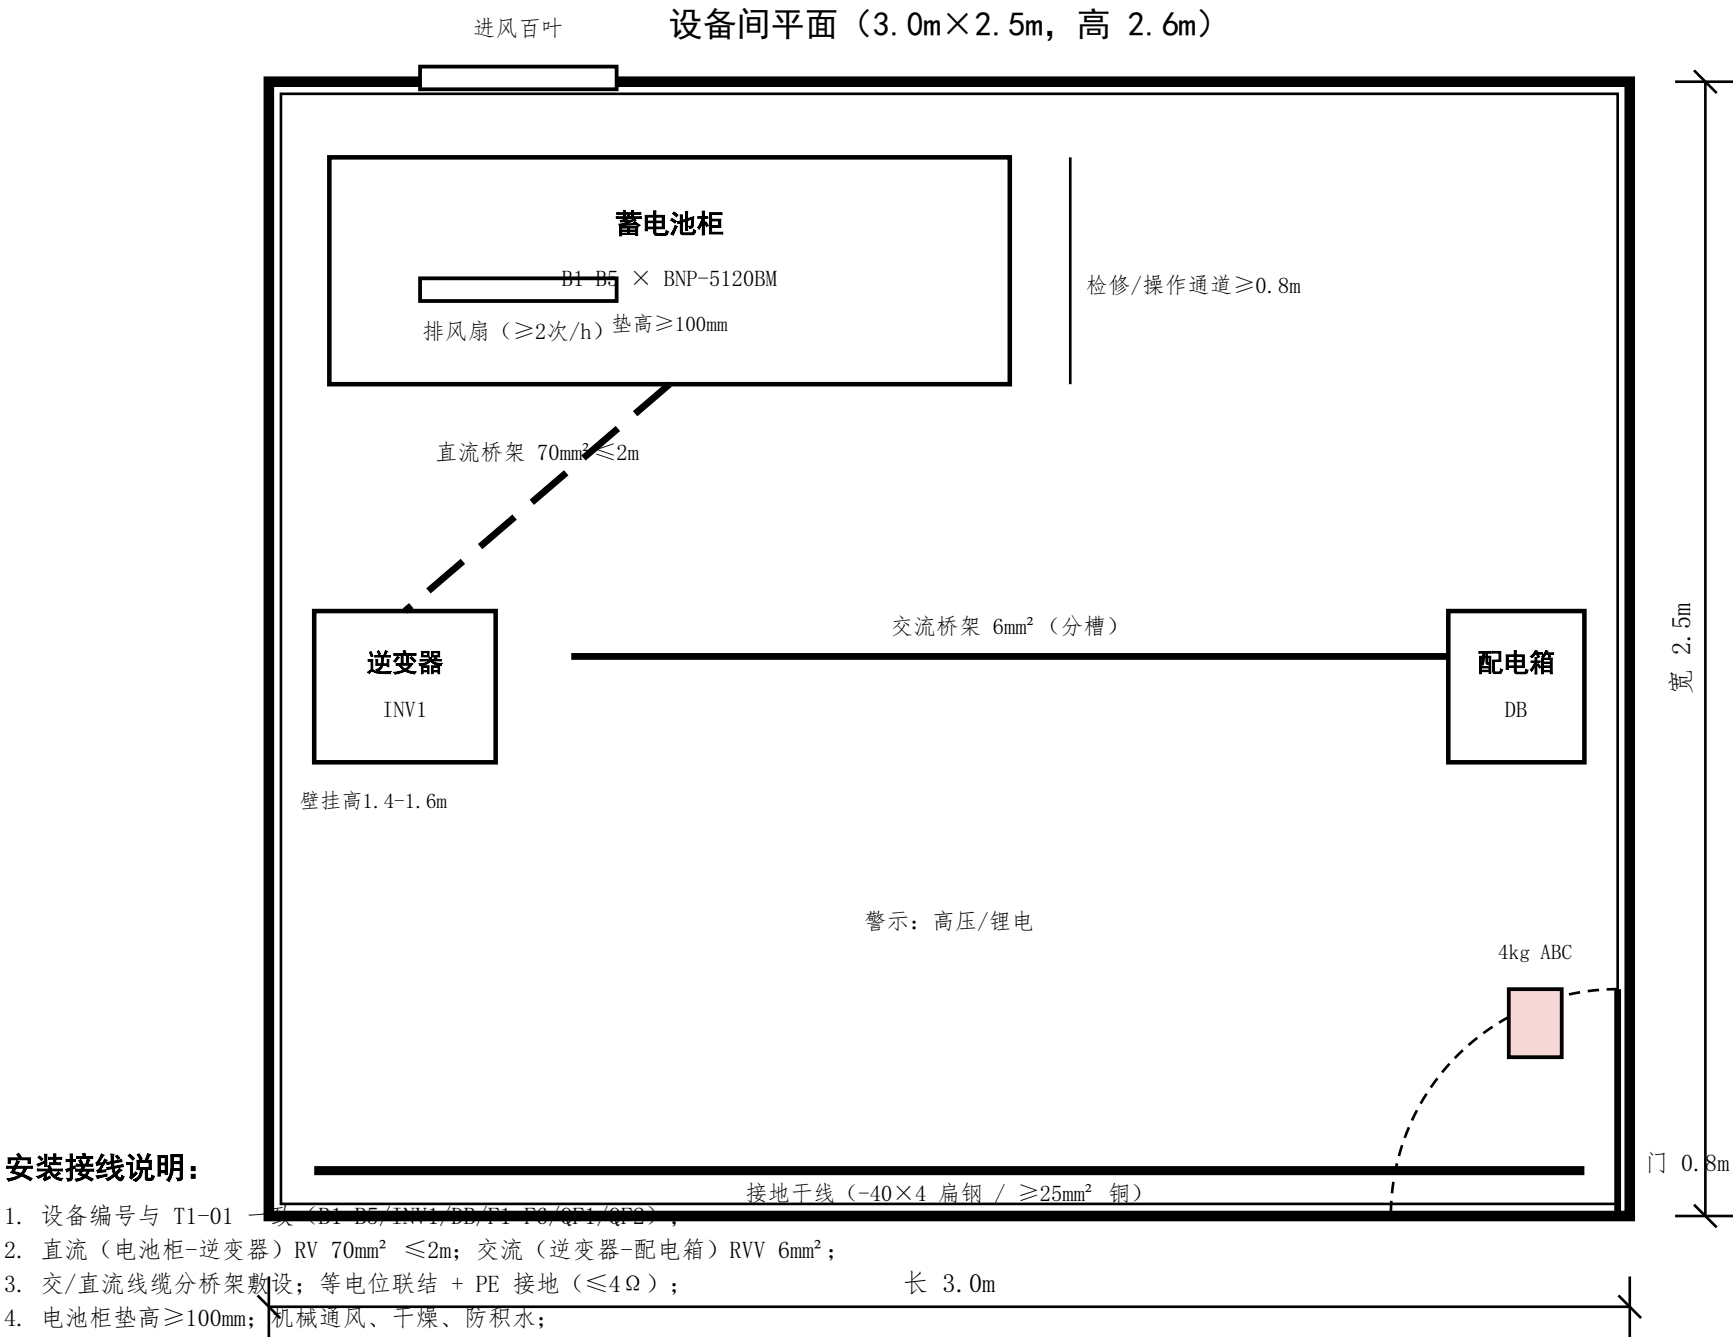

|         |             |         |               |
|---------|-------------|---------|---------------|
| 哈尔滨工业大学 | 设备间平面及安装接线图 | 图号      | T1-03         |
| 设计：____ | 制图：____     | 审核：____ | 日期 2026-09-03 |
| 学号：____ | 班级：____     | 版本 A    | 页次 1/1        |
| 比例      | 1:25        | 单位：mm   |               |