


户用离网光伏发电系统——设备间平面及安装接线图

拉萨/兰州/哈尔滨差异化设计（拉萨） · A3

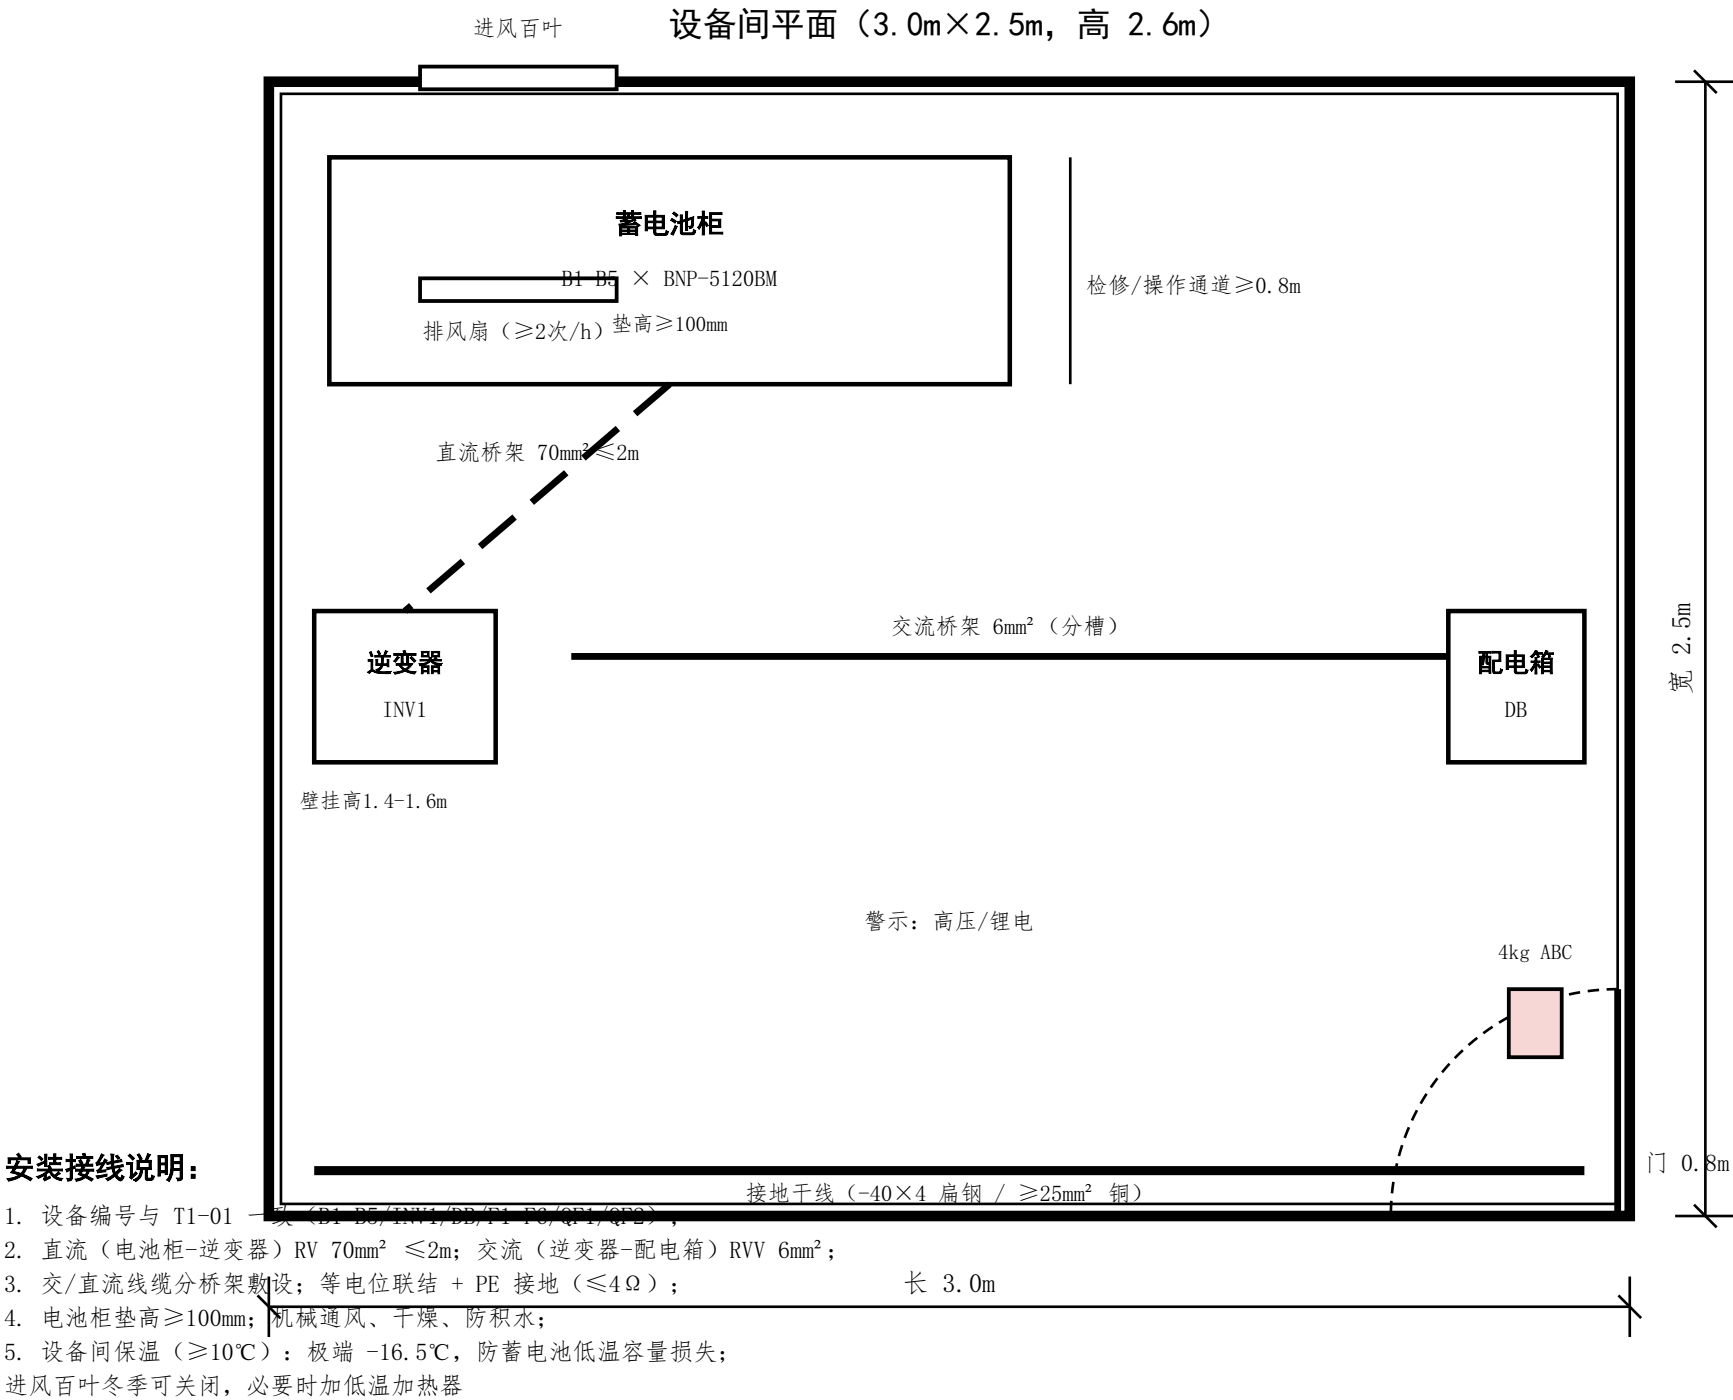

哈尔滨工业大学	设备间平面及安装接线图	图号	T1-03
设计：____	制图：____	审核：____	日期 2026-09-03
学号：____	班级：____	版本 A	页次 1/1
比例	1:25	单位：mm	