



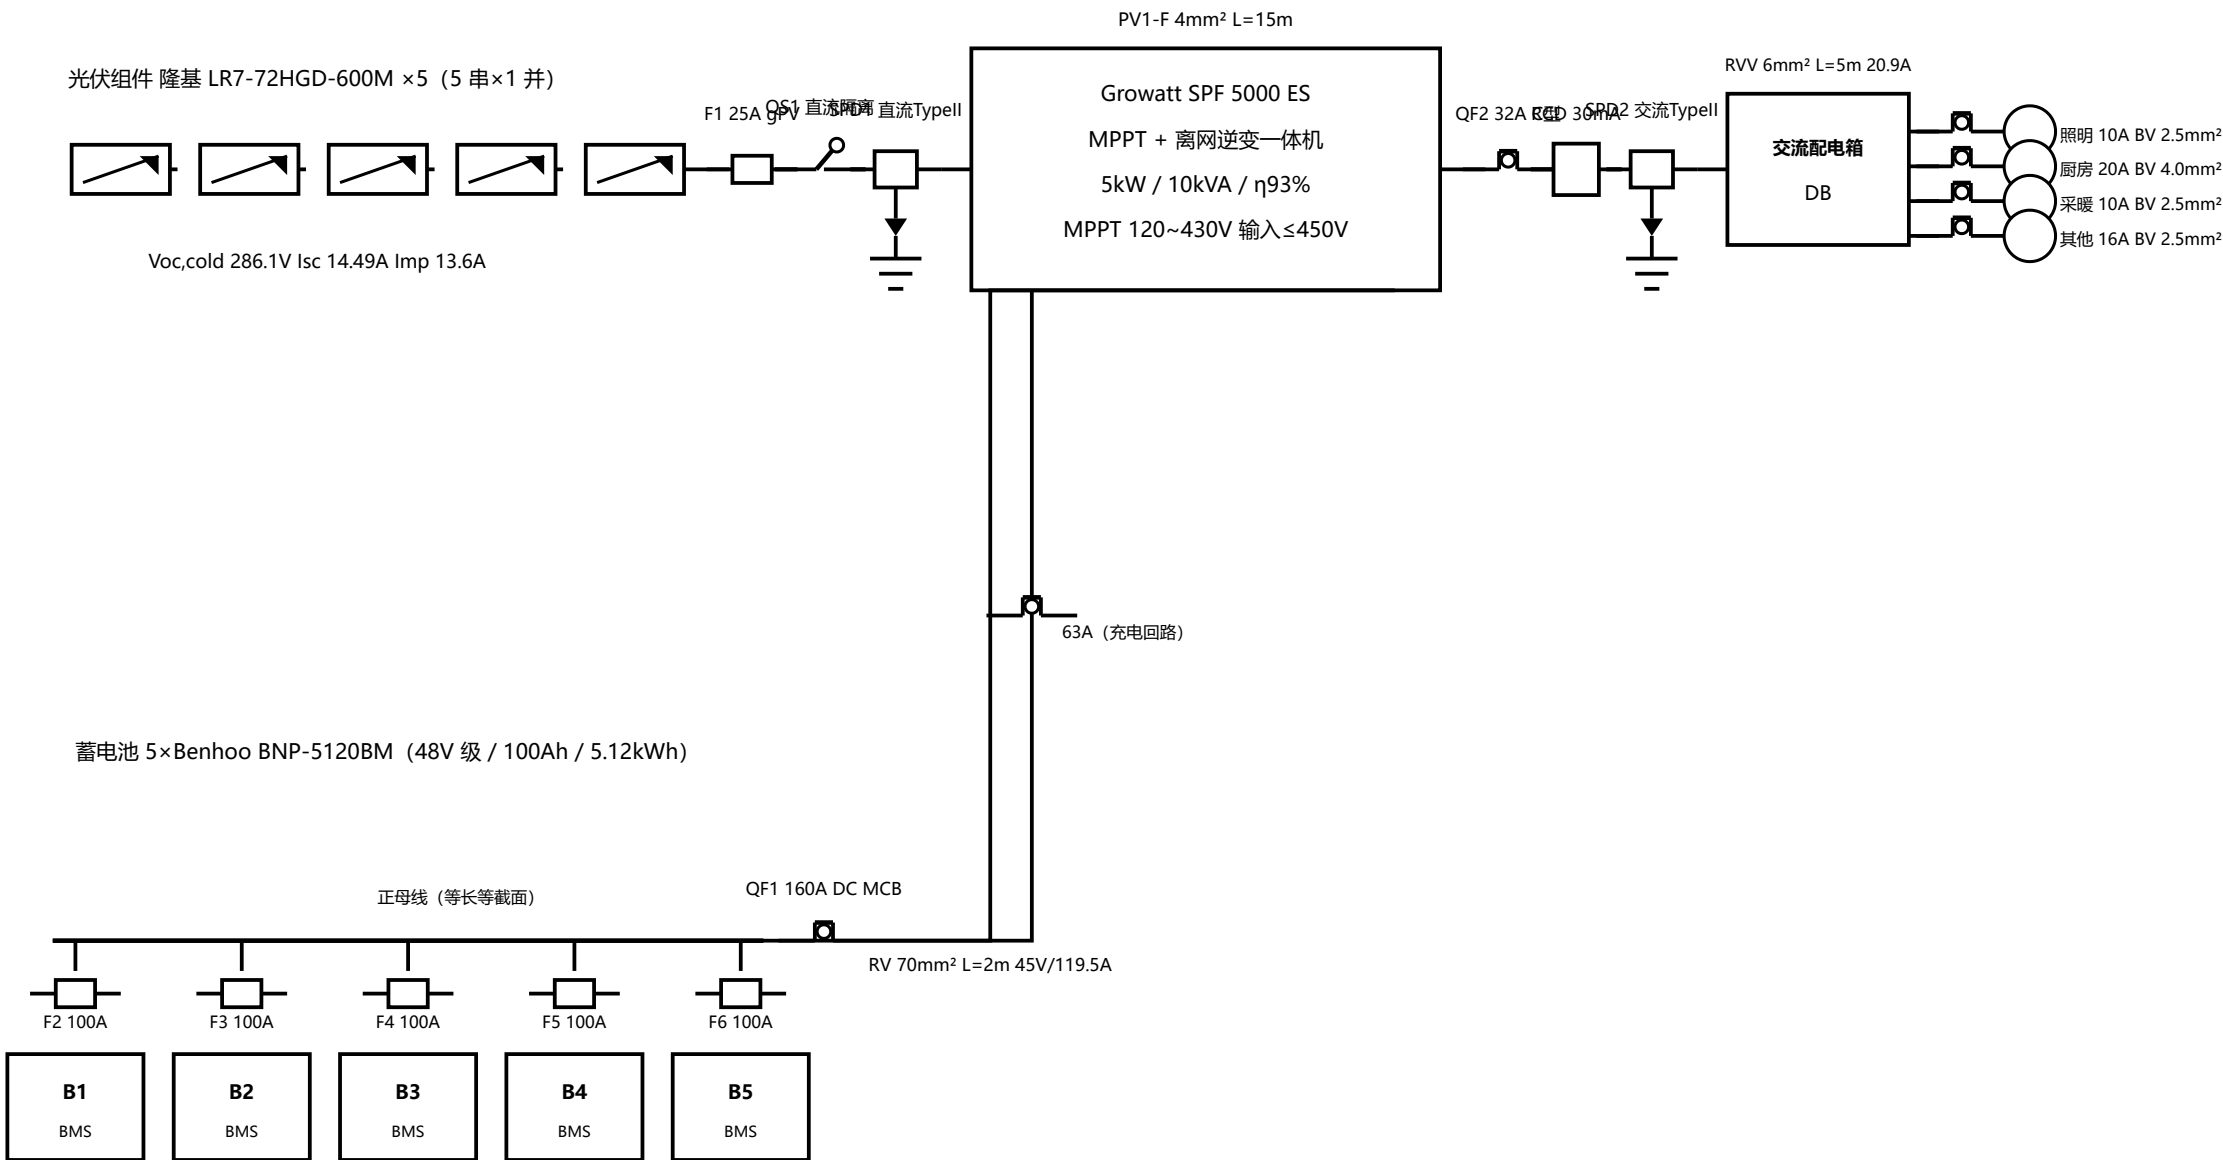

保护接地 (PE) : 组件边框、支架、设备外壳; 等电位联结 (≥6mm²) ; 接地电阻≤4Ω
拉萨差异化: 少雷区两级 SPD; 高海拔 3650m 逆变器降额校核; 设备间保温≥10℃

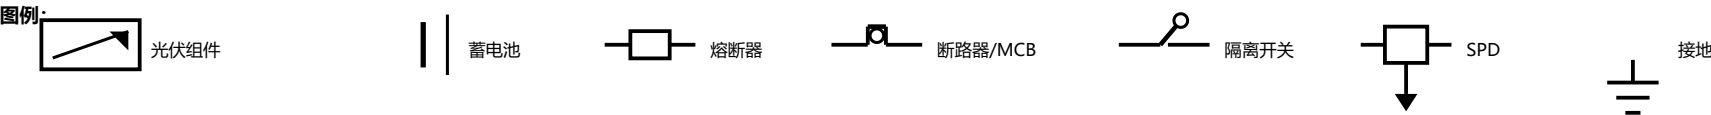

图名	系统电气主接线图 (拉萨)	姓名 ____	日期
图号	T1-01	学号 ____	2026-09-07
比例	无比例	版本 A	单位 哈工大 (深圳)