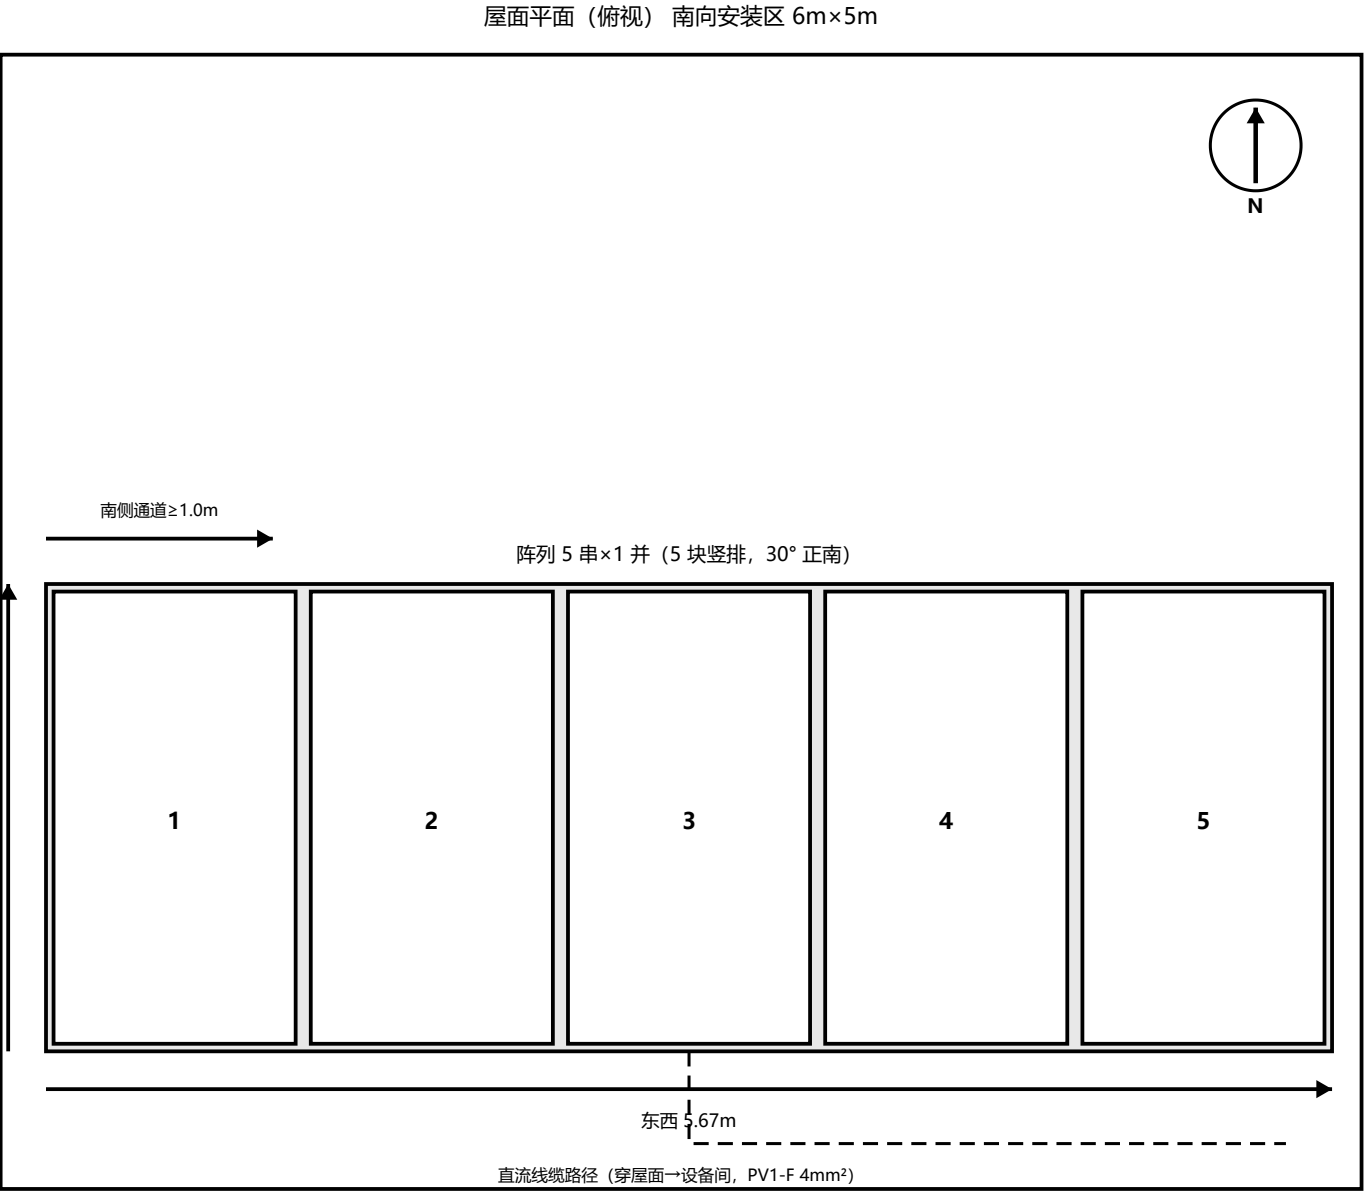


排距（扩排）： $D=2.382 \cdot \cos 30^\circ + 2.382 \cdot \sin 30^\circ / \tan 21.5^\circ = 5.09\text{m}$ （ $\approx 2.13 \times L$ ，冬至 9:00）

支架校核： $w_k=0.31\text{kN/m}^2$ ；铝导轨6063-T5 简支 $L_b=1.2\text{m}$ ： $\sigma=5.6\text{MPa} \leq 85$ ， $f=0.21\text{mm} \leq L/200$

图名	光伏阵列及支架布置图（拉萨）	姓名 ____	日期
图号	T1-02	学号 ____	2026-09-07
比例	1:50	版本 A	单位 哈工大（深圳）