



屋面平面（俯视） 可用安装区约 12m×5m（南向）

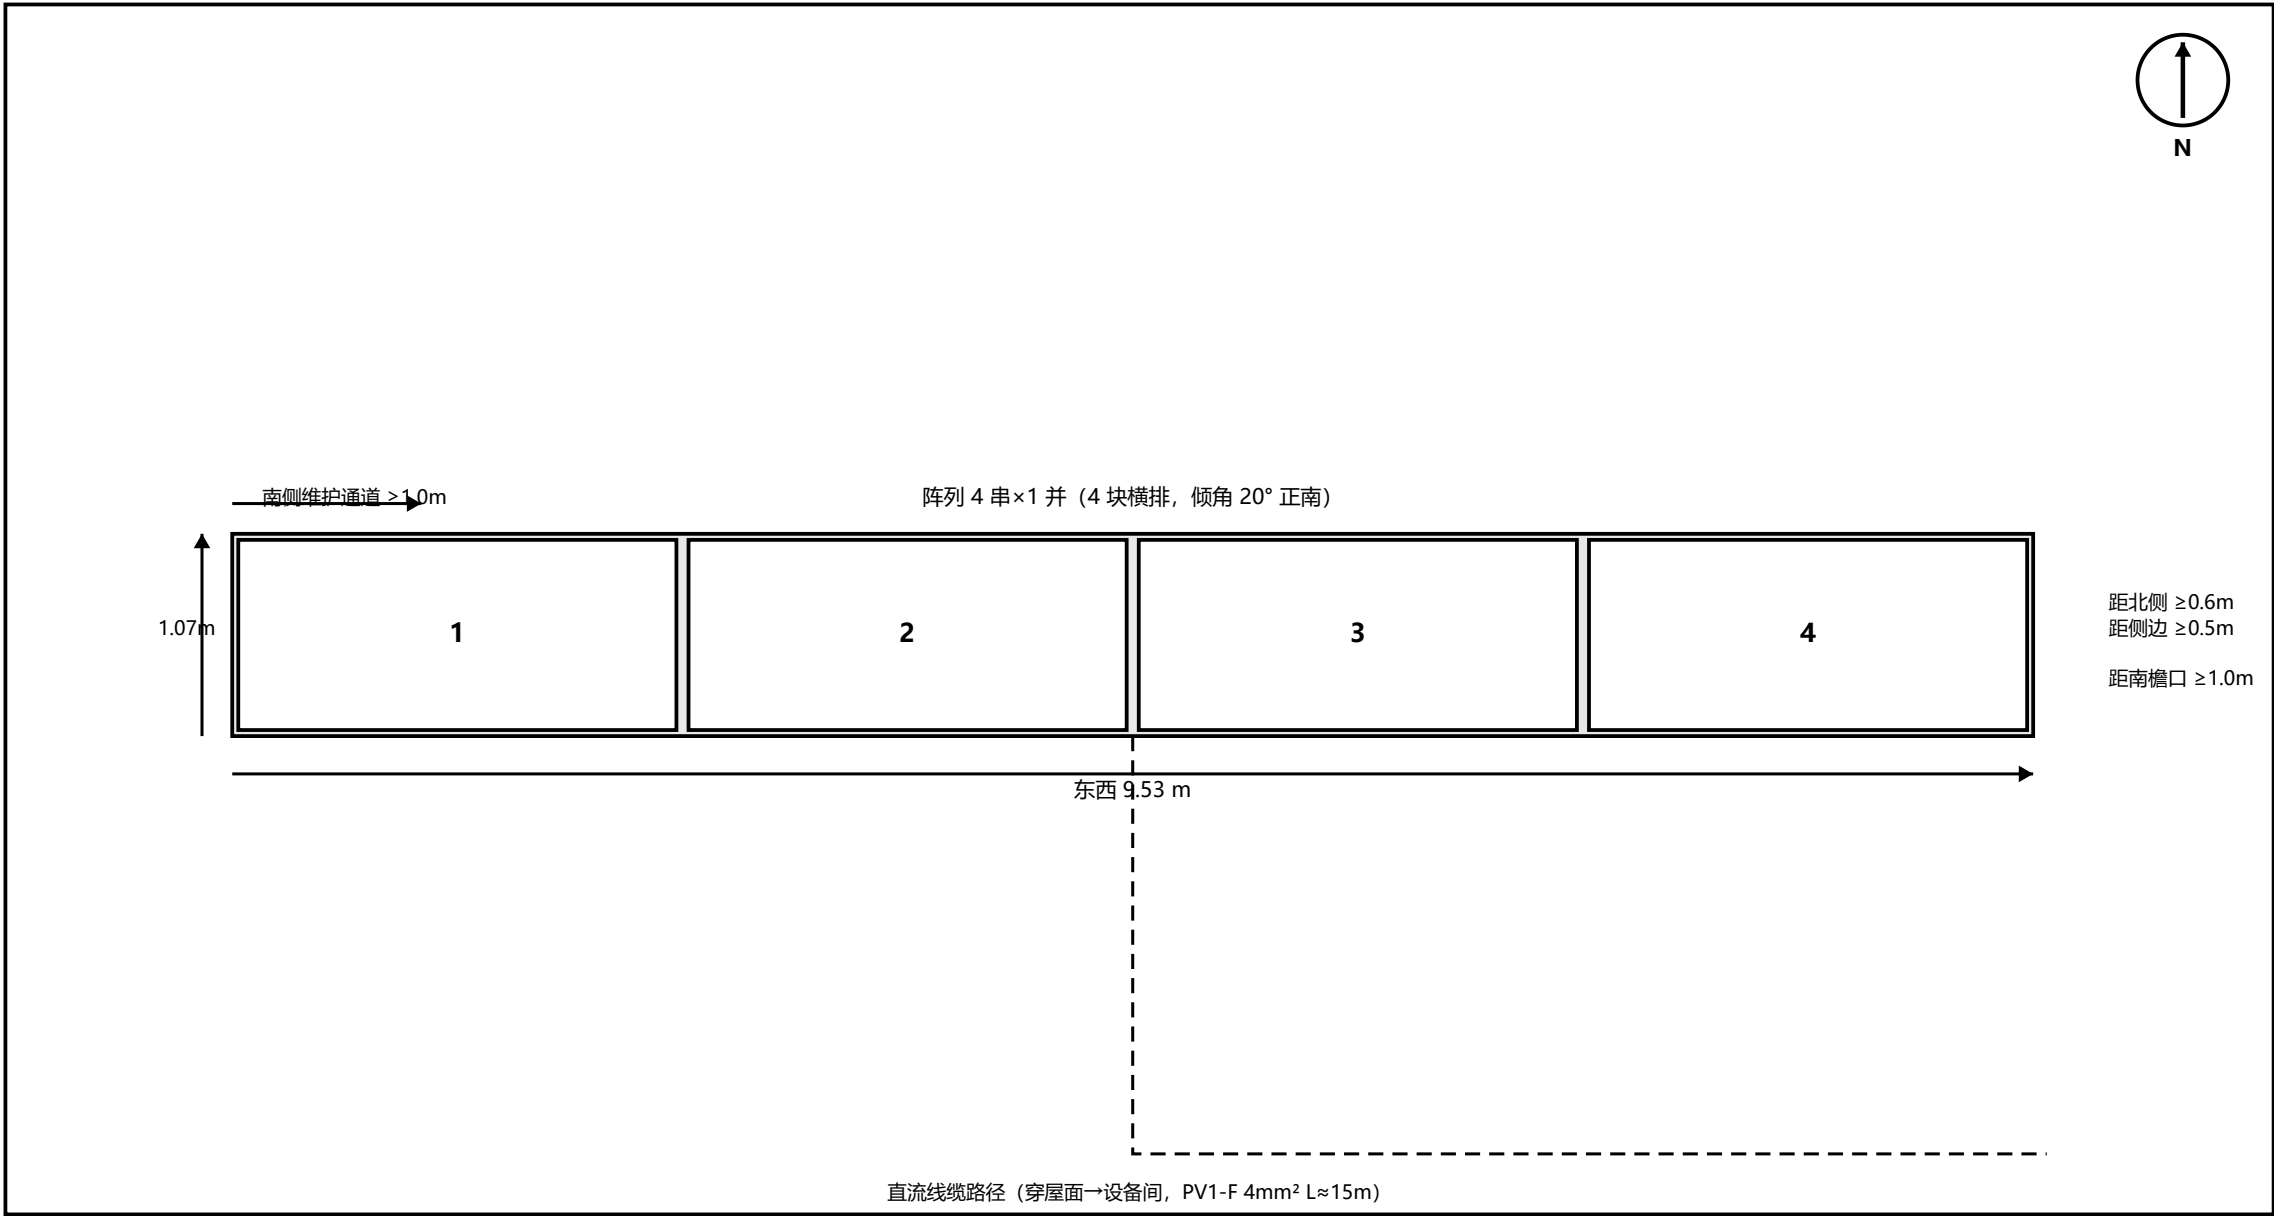

阵列剖面（南-北，A-A）：

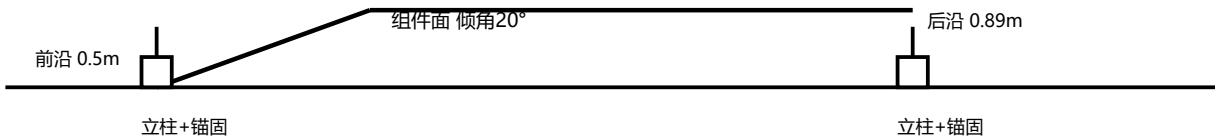

排间节距（扩排）： $D=L\cdot\cos 20^{\circ}+L\cdot\sin 20^{\circ}/\tan 26.5^{\circ}=1.84\text{m}$ （ $\approx 1.63\times L$ ）

导轨：铝 6063-T5， $\sigma=24.3\text{MPa}\leq 85\text{MPa}$ ， $f=0.88\text{mm}\leq L/200$ （W8 校核）

图名	光伏阵列及支架布置图	姓名	____	日期
图号	T1-02	学号	____	2026-06-03 哈工大（深圳）
比例	1:100	版本	A	单位