


表达：直流正负分线；交流支路为L+N单线；实心点为连接点，交叉无点不连接。

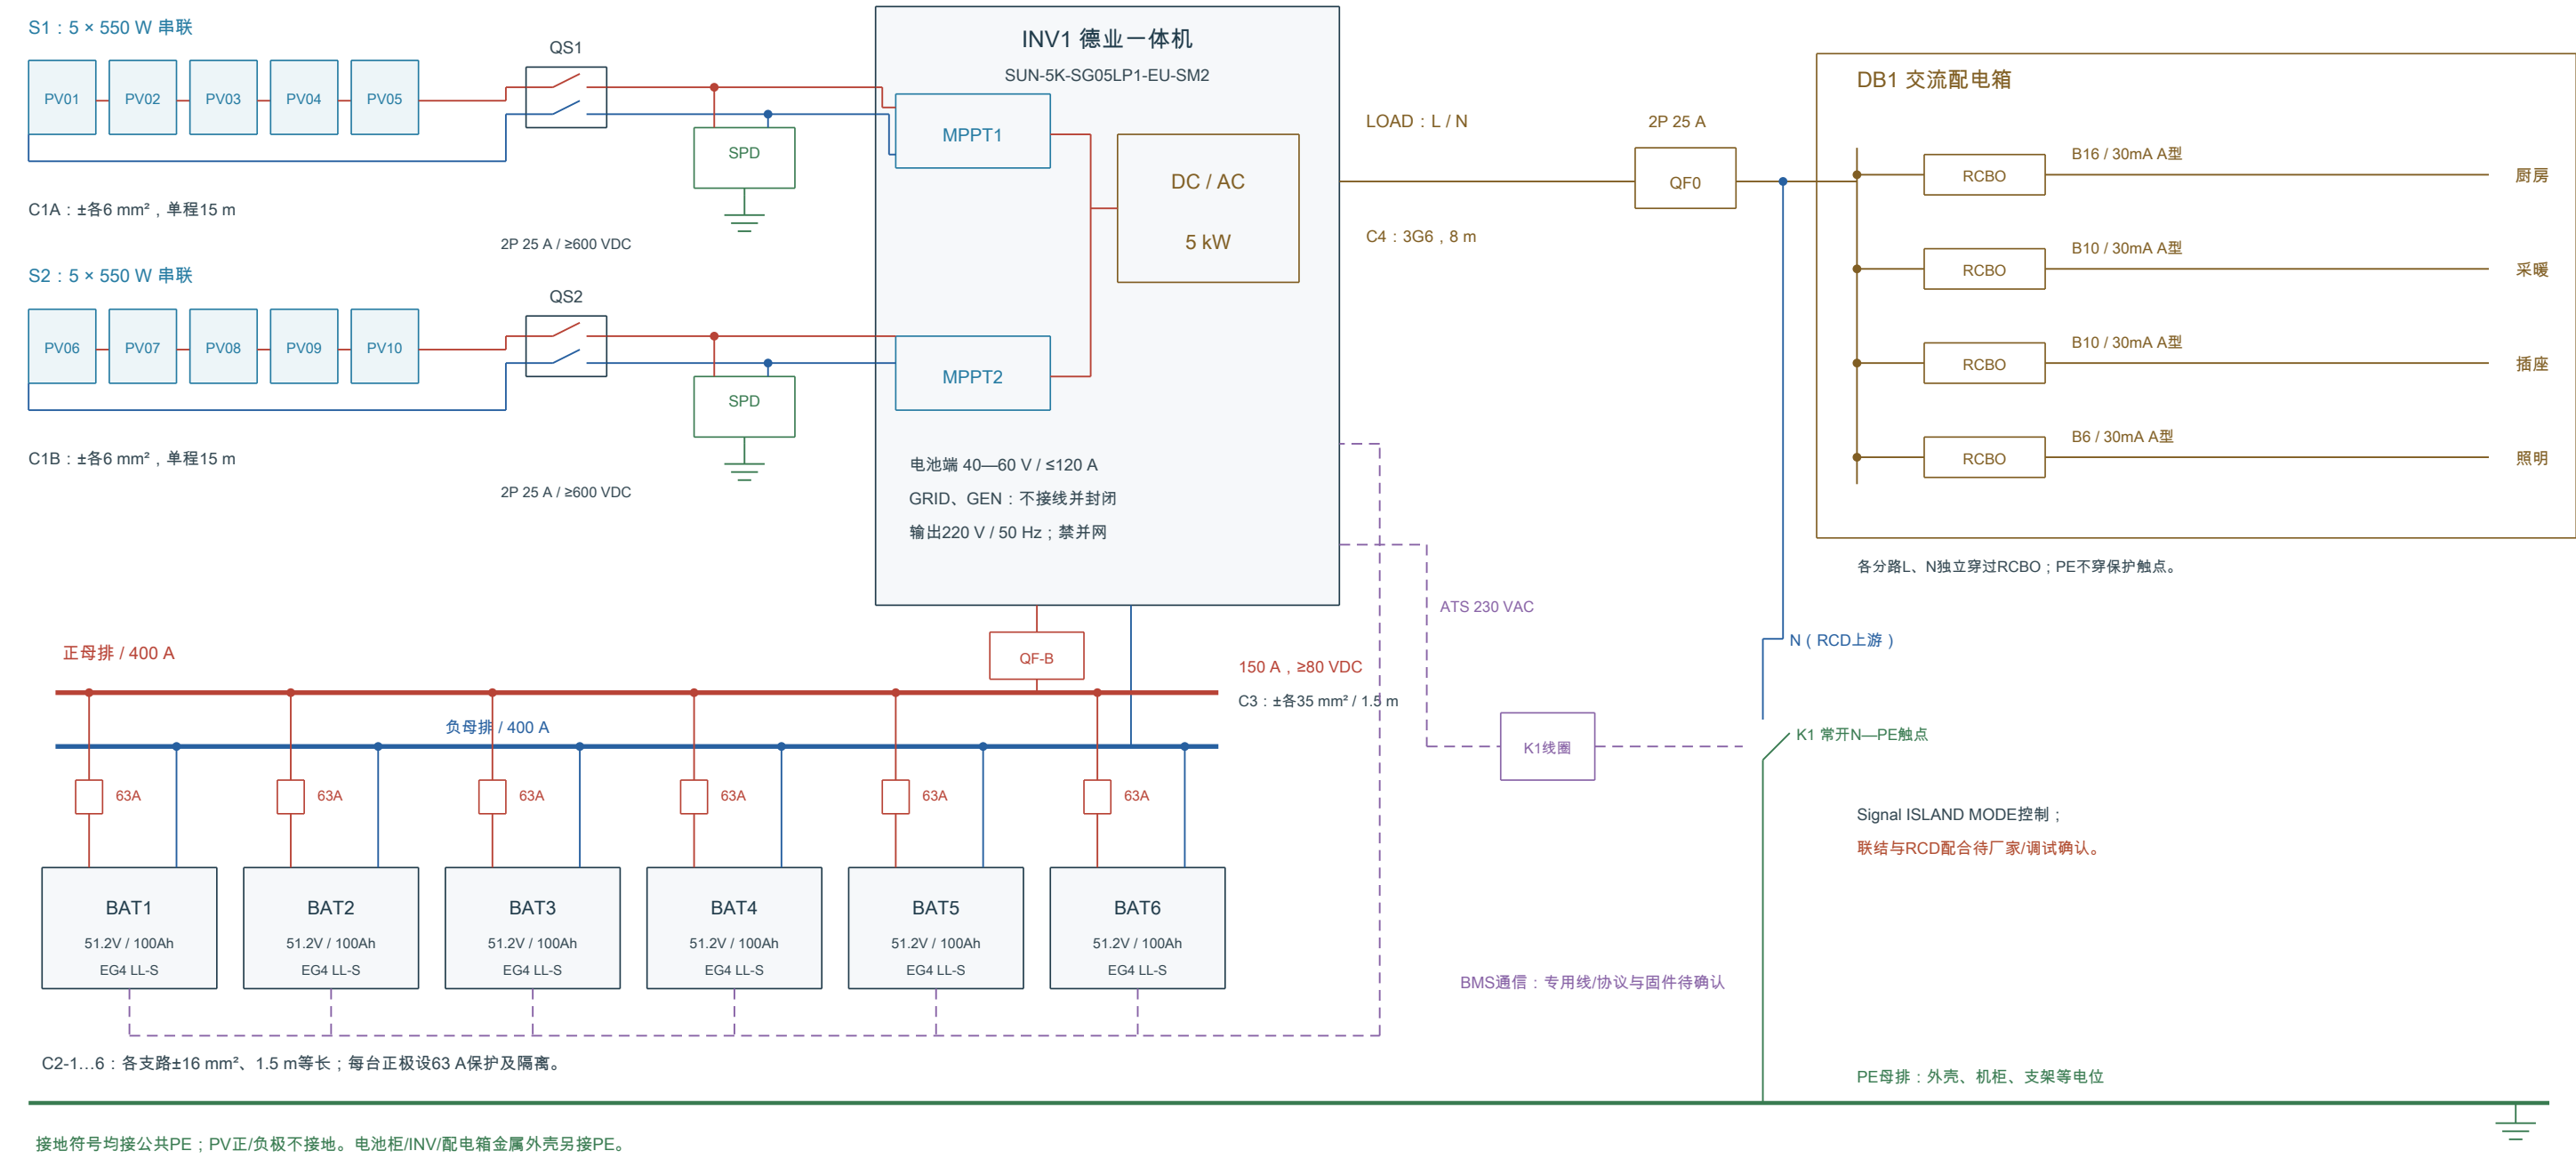

关键待核：五串Vmp(STC)=209.75 V；手册满载MPPT范围300—425 V。

本图仅为拓扑初稿；功率降额未核定，5.50 kWp与恢复时间不得视作最终保证。

保护初选：150 A与35 mm²须核对实际载流量；分断能力/熔断I²t尚待产品资料。

电池6台共600 Ah/30.72 kWh；每日SOC截止20%，CCL/DCL限流优先。

图例：红=DC+，蓝=DC-，棕=AC，绿=PE，紫=通信/控制。

SPD：每PV端初选T2、Ucpv350 V；机内/外部配合待核。

总线/分路线径均为铜线初选；交流回路单线代表L+N。

高负荷烧水前关电暖器；无市电/发电机接入。

系统电气原理与接线图

5.50 kWp / 30.72 kWh / 5 kW | 图号、设备编号与计算稿对应

用途：方案讨论与答辩。假设及待核事项见图内说明，非施工定稿。

图号 E-01

版本 R0

比例 示意 / A3

2026-09-10