



屋顶平面 1:50 | 尺寸单位mm

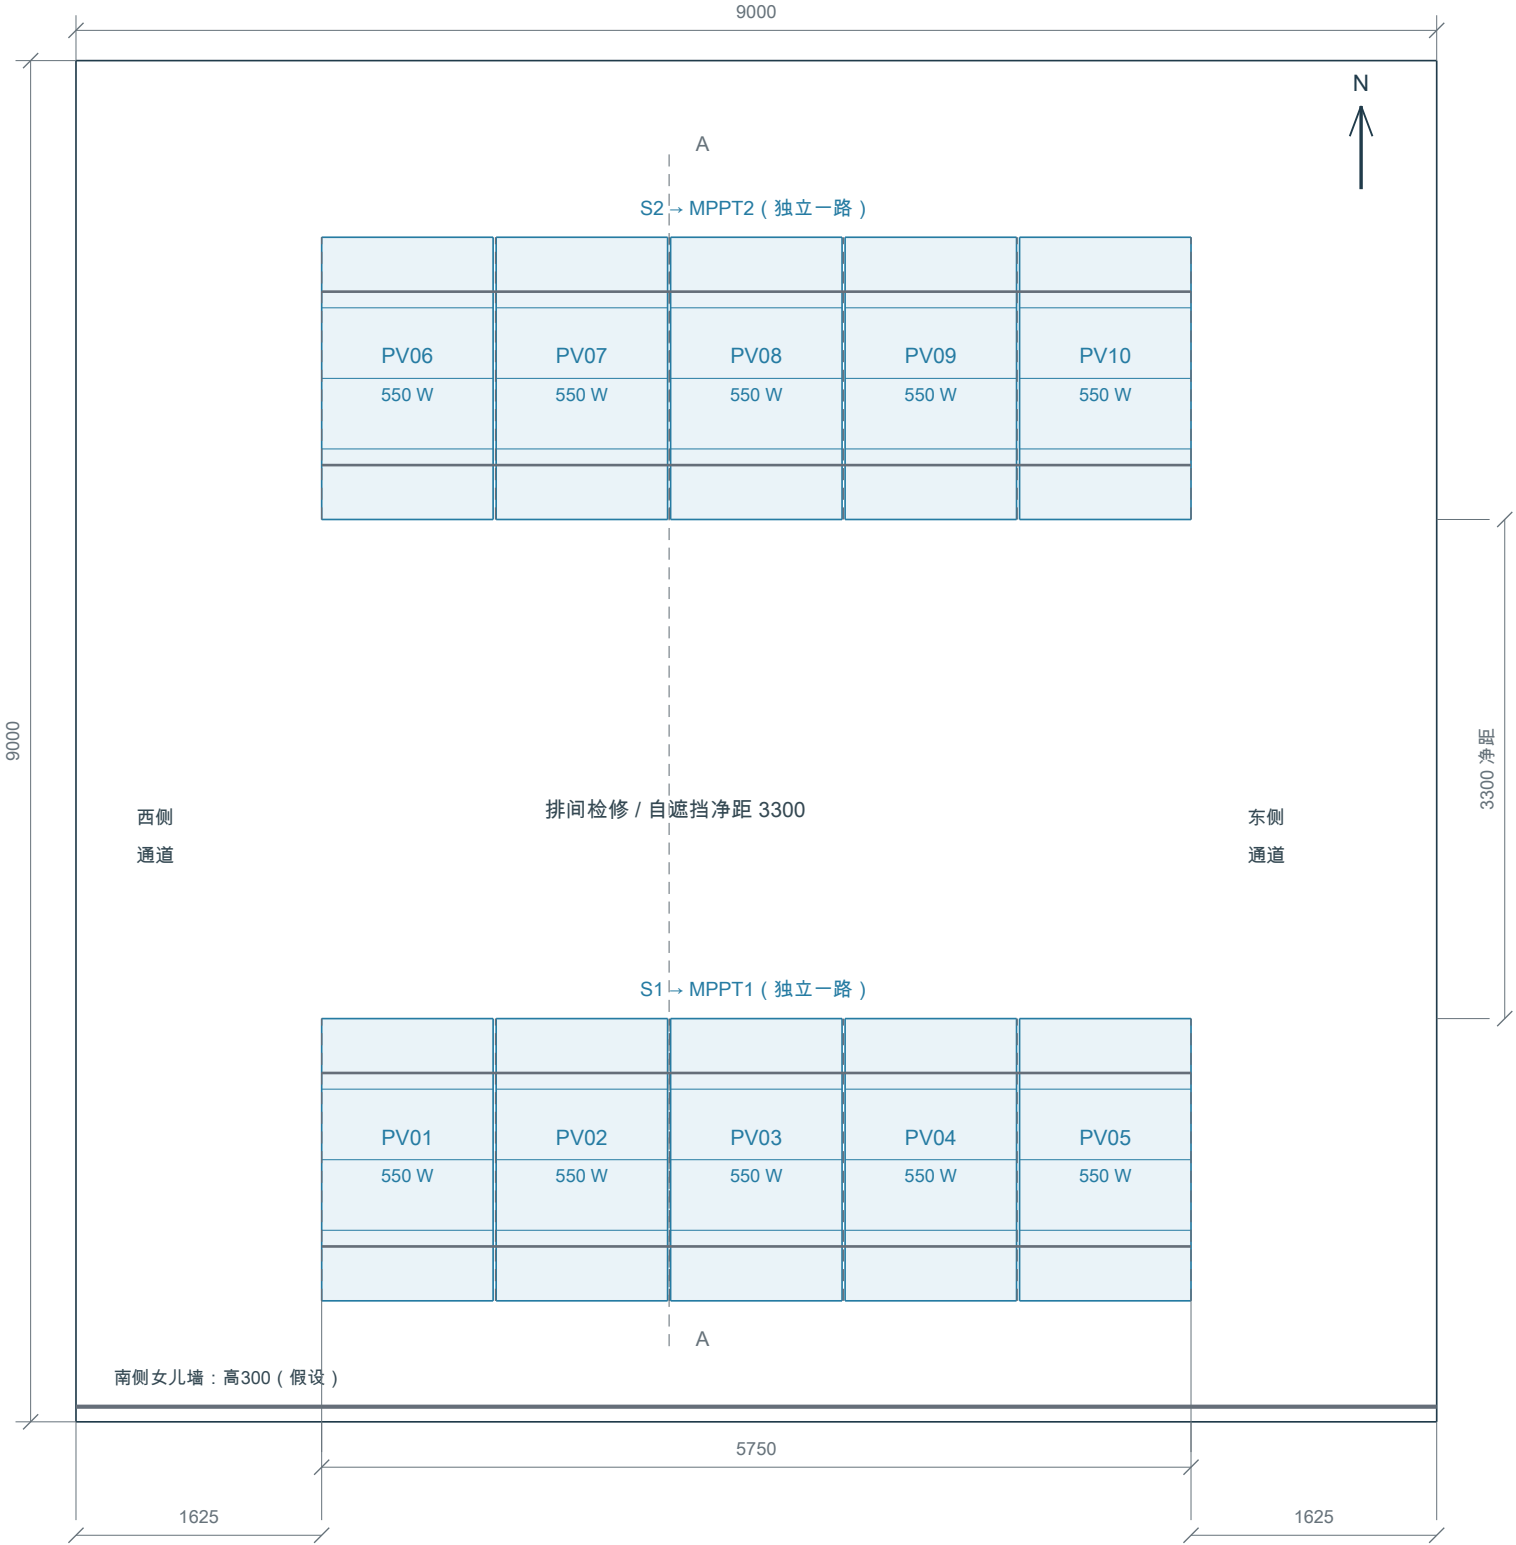

南北剖面 A—A 1:50

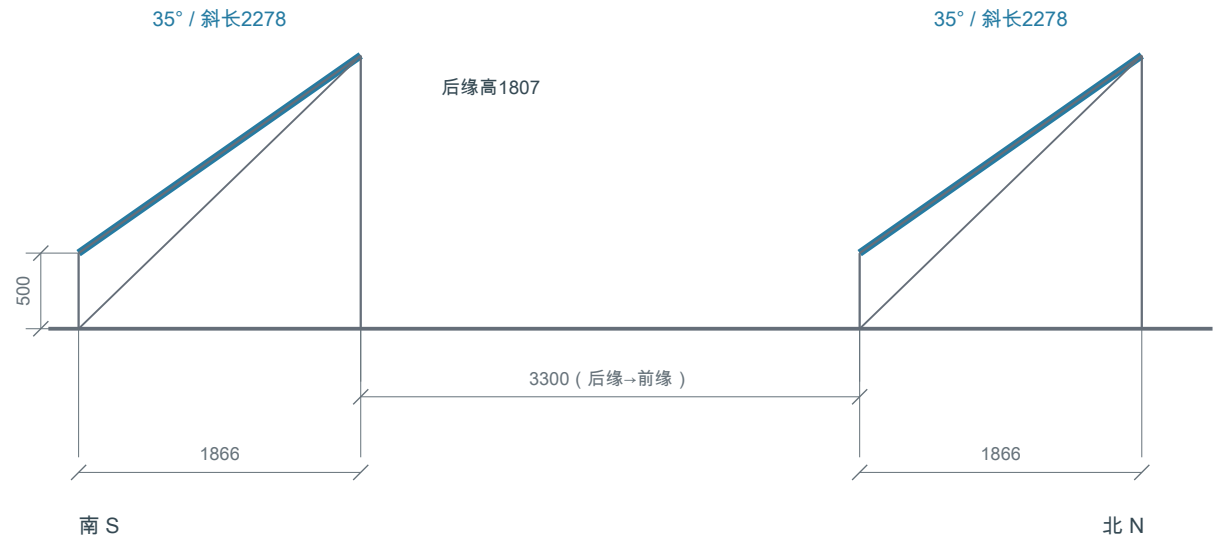

支架与图纸参数

- 01 每排5块竖向组件, 缝20; 每排6樘支承, 共12樘。
- 02 每排2道檩条, 每道5750; 共4道, 总长23000。
- 03 支承间距约1150; 梁计算跨度上取1200。
- 04 Q235矩形钢管60×40×3, 60方向竖置 (初选)。
- 05 檩条示意依据1400安装孔纵向间距, 实际夹持按厂家。
- 06 冬至太阳时09—15: 净距需求约3165, 采用3300。
- 07 屋顶为9000×9000教学假设; 邻楼/山体遮挡未勘测。

待核事项

- 风吸2.0 kPa、下压0.65 kPa为教学输入, 非兰州实测。
- 本图不定锚栓直径、数量、配重或屋面连接做法。
- 单根檩条计算不代替整体抗风、抗震、承载和防水审查。
- MPPT电压段功率待确认, 组件数量与布置可能随之调整。

屋顶方阵及支架布置图

5.50 kWp / 30.72 kWh / 5 kW | 图号、设备编号与计算稿对应

用途: 方案讨论与答辩。假设及待核事项见图内说明, 非施工定稿。

图号 M-01

版本 R0

比例 1:50 / A3

2026-09-10