



设备间平面 1:20 | 西南角为坐标原点

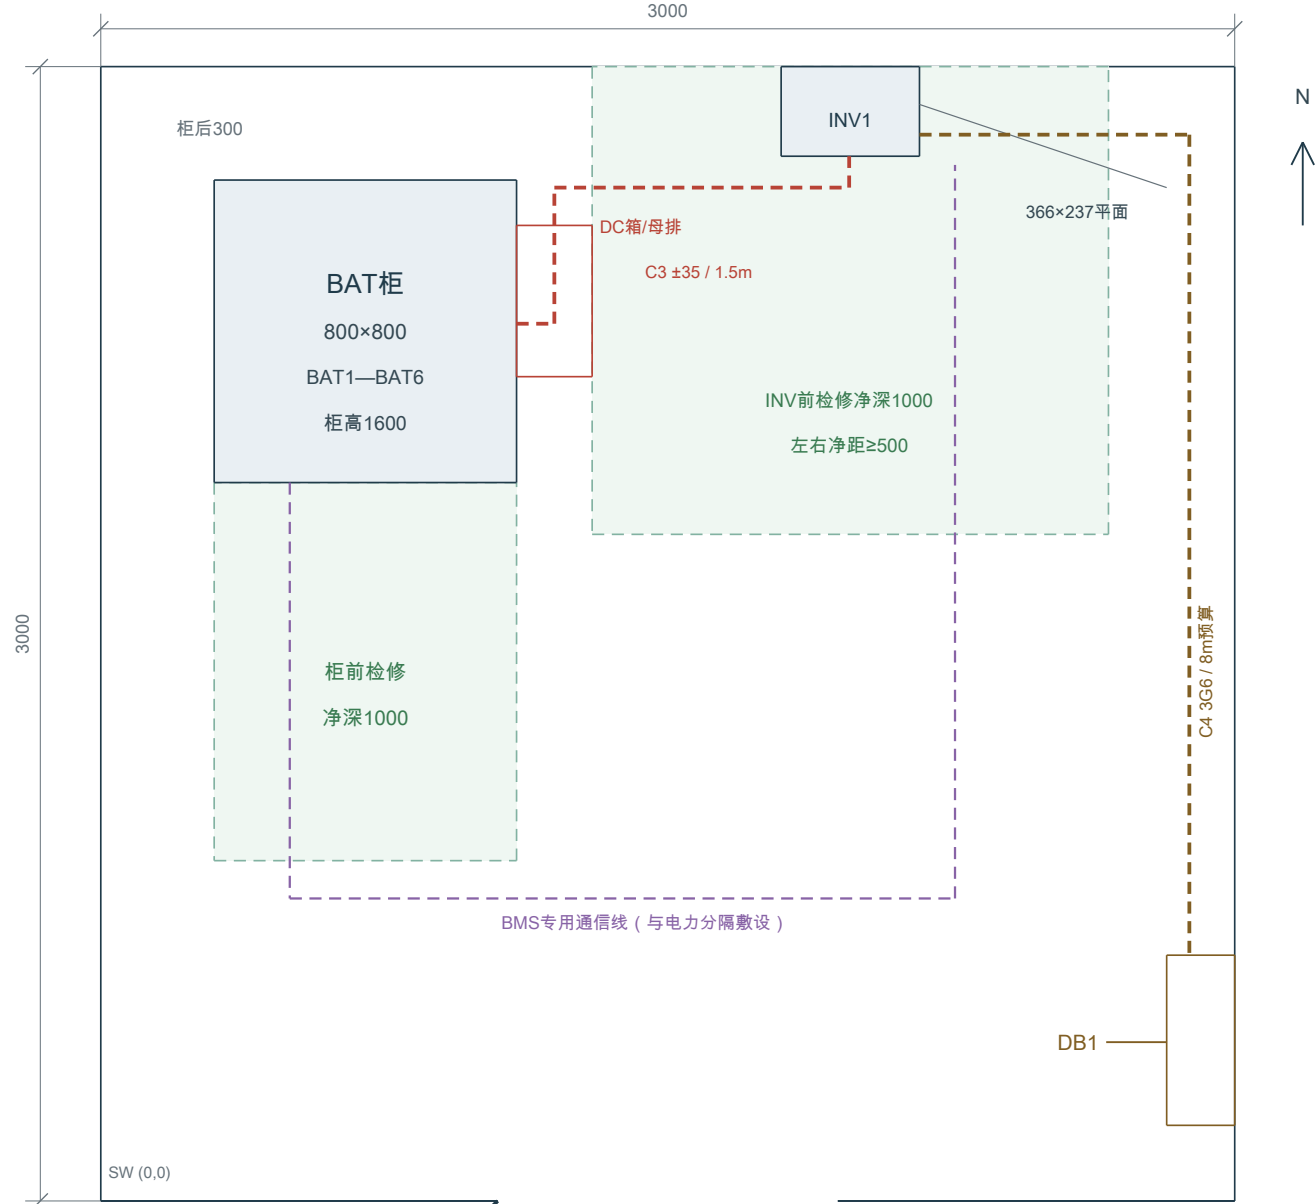

门净宽900
向外开（示意）

颜色虚线为路由示意，不代表已实测线长；绕行/上下翻后重算。
图内维护区域保持畅通。机柜实际导轨、承重与厂家散热间距待确认。

北墙立面 1:20 | 层高2800（假设）

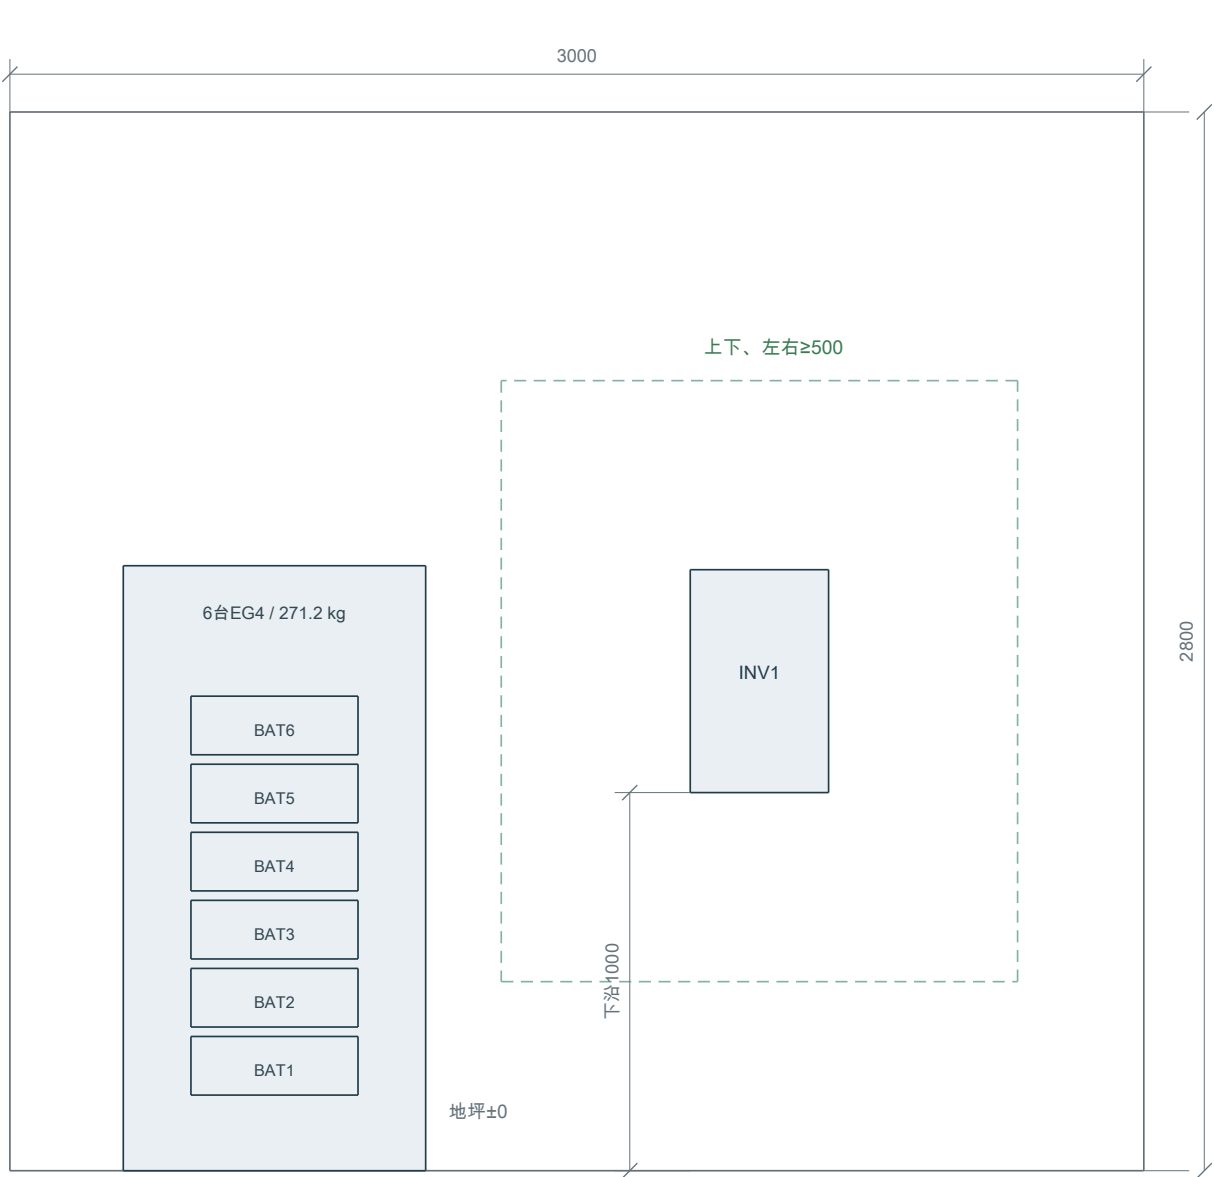

布置与温控条件

柜体800×800×1600，承重≥400 kg为初选，非已订购型号。

模块尺寸155×442×490；INV尺寸366×589.5×237。

已有建筑供暖维持电池10—40℃，额外电加热不计入容量。

排风需求约171 m³/h；选≥200 m³/h、12W仅为预算。

夏季通风不足时需降载/制冷，并回算能耗；不得宣称已验证。

机柜重、地板承载、接地连续性、BMS/保护联调待落实。

设备间平面及安装接线图

5.50 kWp / 30.72 kWh / 5 kW | 图号、设备编号与计算稿对应

用途：方案讨论与答辩。假设及待核事项见图内说明，非施工定稿。

图号 M-02

版本 R0

比例 1:20 / A3

2026-09-10