


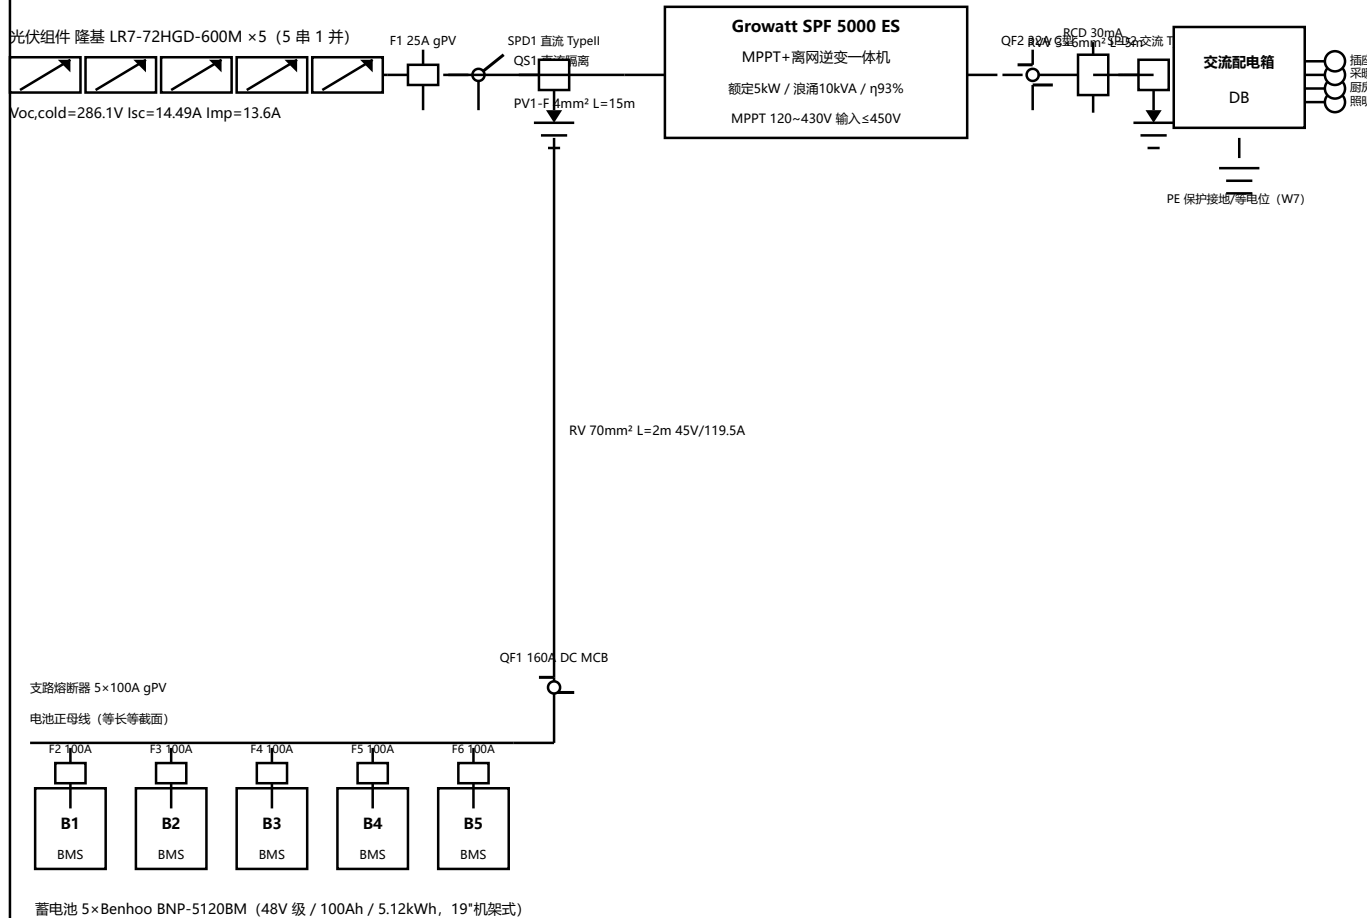

图例:



光伏组件



蓄电池



熔断器



断路器/RCB



隔离开关



SPD



接地

图名	系统电
图号	T1-01
比例	无比例