



屋面平面（俯视） 可用安装区约 7m×6m（南向）

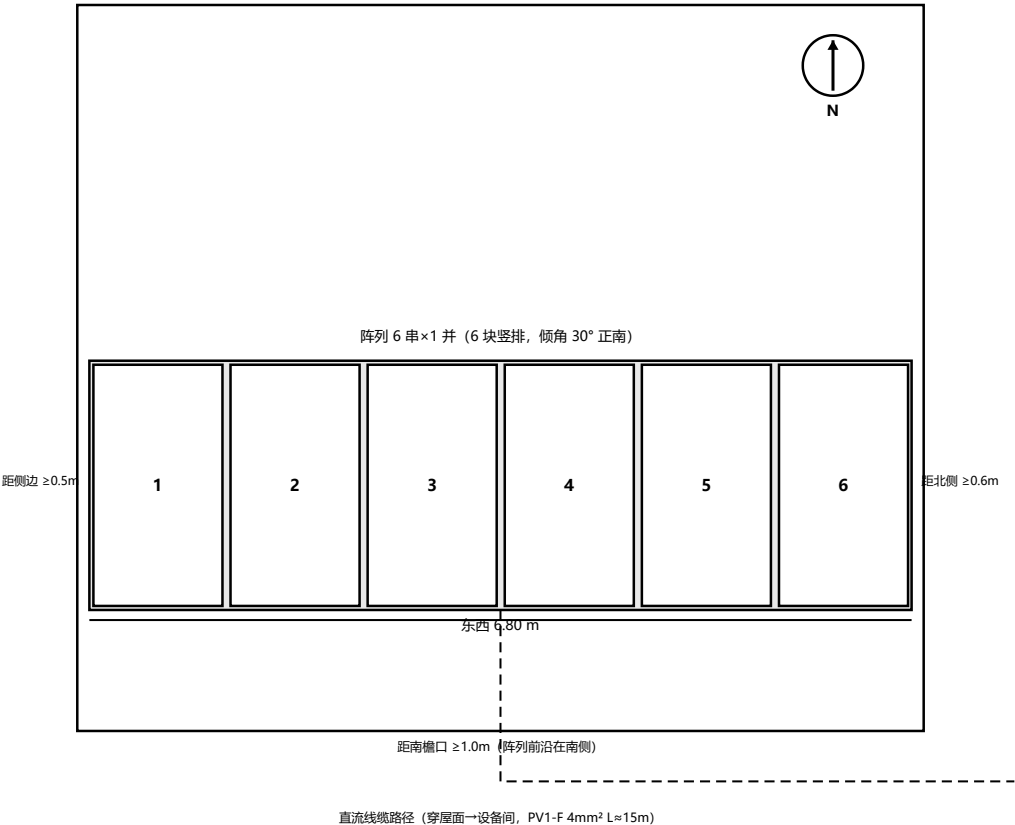

直流线缆路径（穿屋面→设备间，PV1-F 4mm² L≈15m）

阵列剖面（南-北，A-A）：

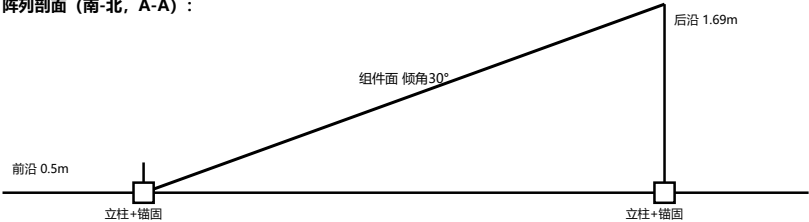

排间节距（扩排）： $D=L\cos30^{\circ}+L\sin30^{\circ}/\tan\alpha=5.98\text{m}$ （ $\approx 2.51\times L$ ）
导轨：铝 6063-T5， $\sigma=9.9\text{MPa}\leq 85\text{MPa}$ ， $f=0.36\text{mm}\leq L/200$ （W8 校核）

图名	光伏阵列
图号	T1-02
比例	1:100