


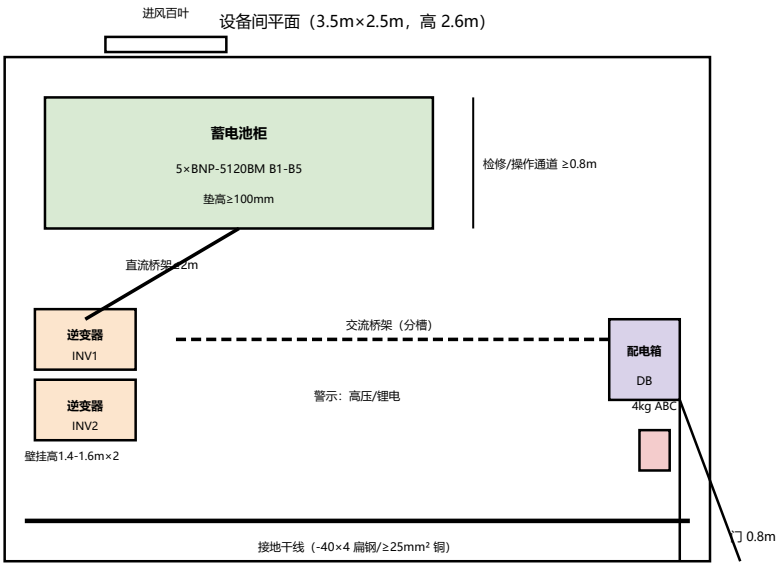

- 安装接线说明:**
- 1) 设备编号与 T1-01 一致 (B1-B5/INV1/DB/F1-F6/QF1/QF2) ;
 - 2) 直流(电池柜-逆变器) 70mm² ≤2m; 交流(逆变器-配电箱) 6mm²;
 - 3) 交/直流线缆分桥架敷设; 等电位联结 + PE 接地;
 - 4) 电池柜垫高 ≥100mm; 设备间机械通风、干燥、防积水;
 - 5) 尺寸与检修距离按 W8 布置定案, 消防/警示齐全;
- 保温+加热 (≥10℃) 为硬性前提: 极端 -38.1℃, 防冻禁充;
- 双逆变器并排壁挂 (间隔≥0.2m 散热) , 两路交直流分槽

图名	设备间 ¹
图号	T1-03
比例	1:25